


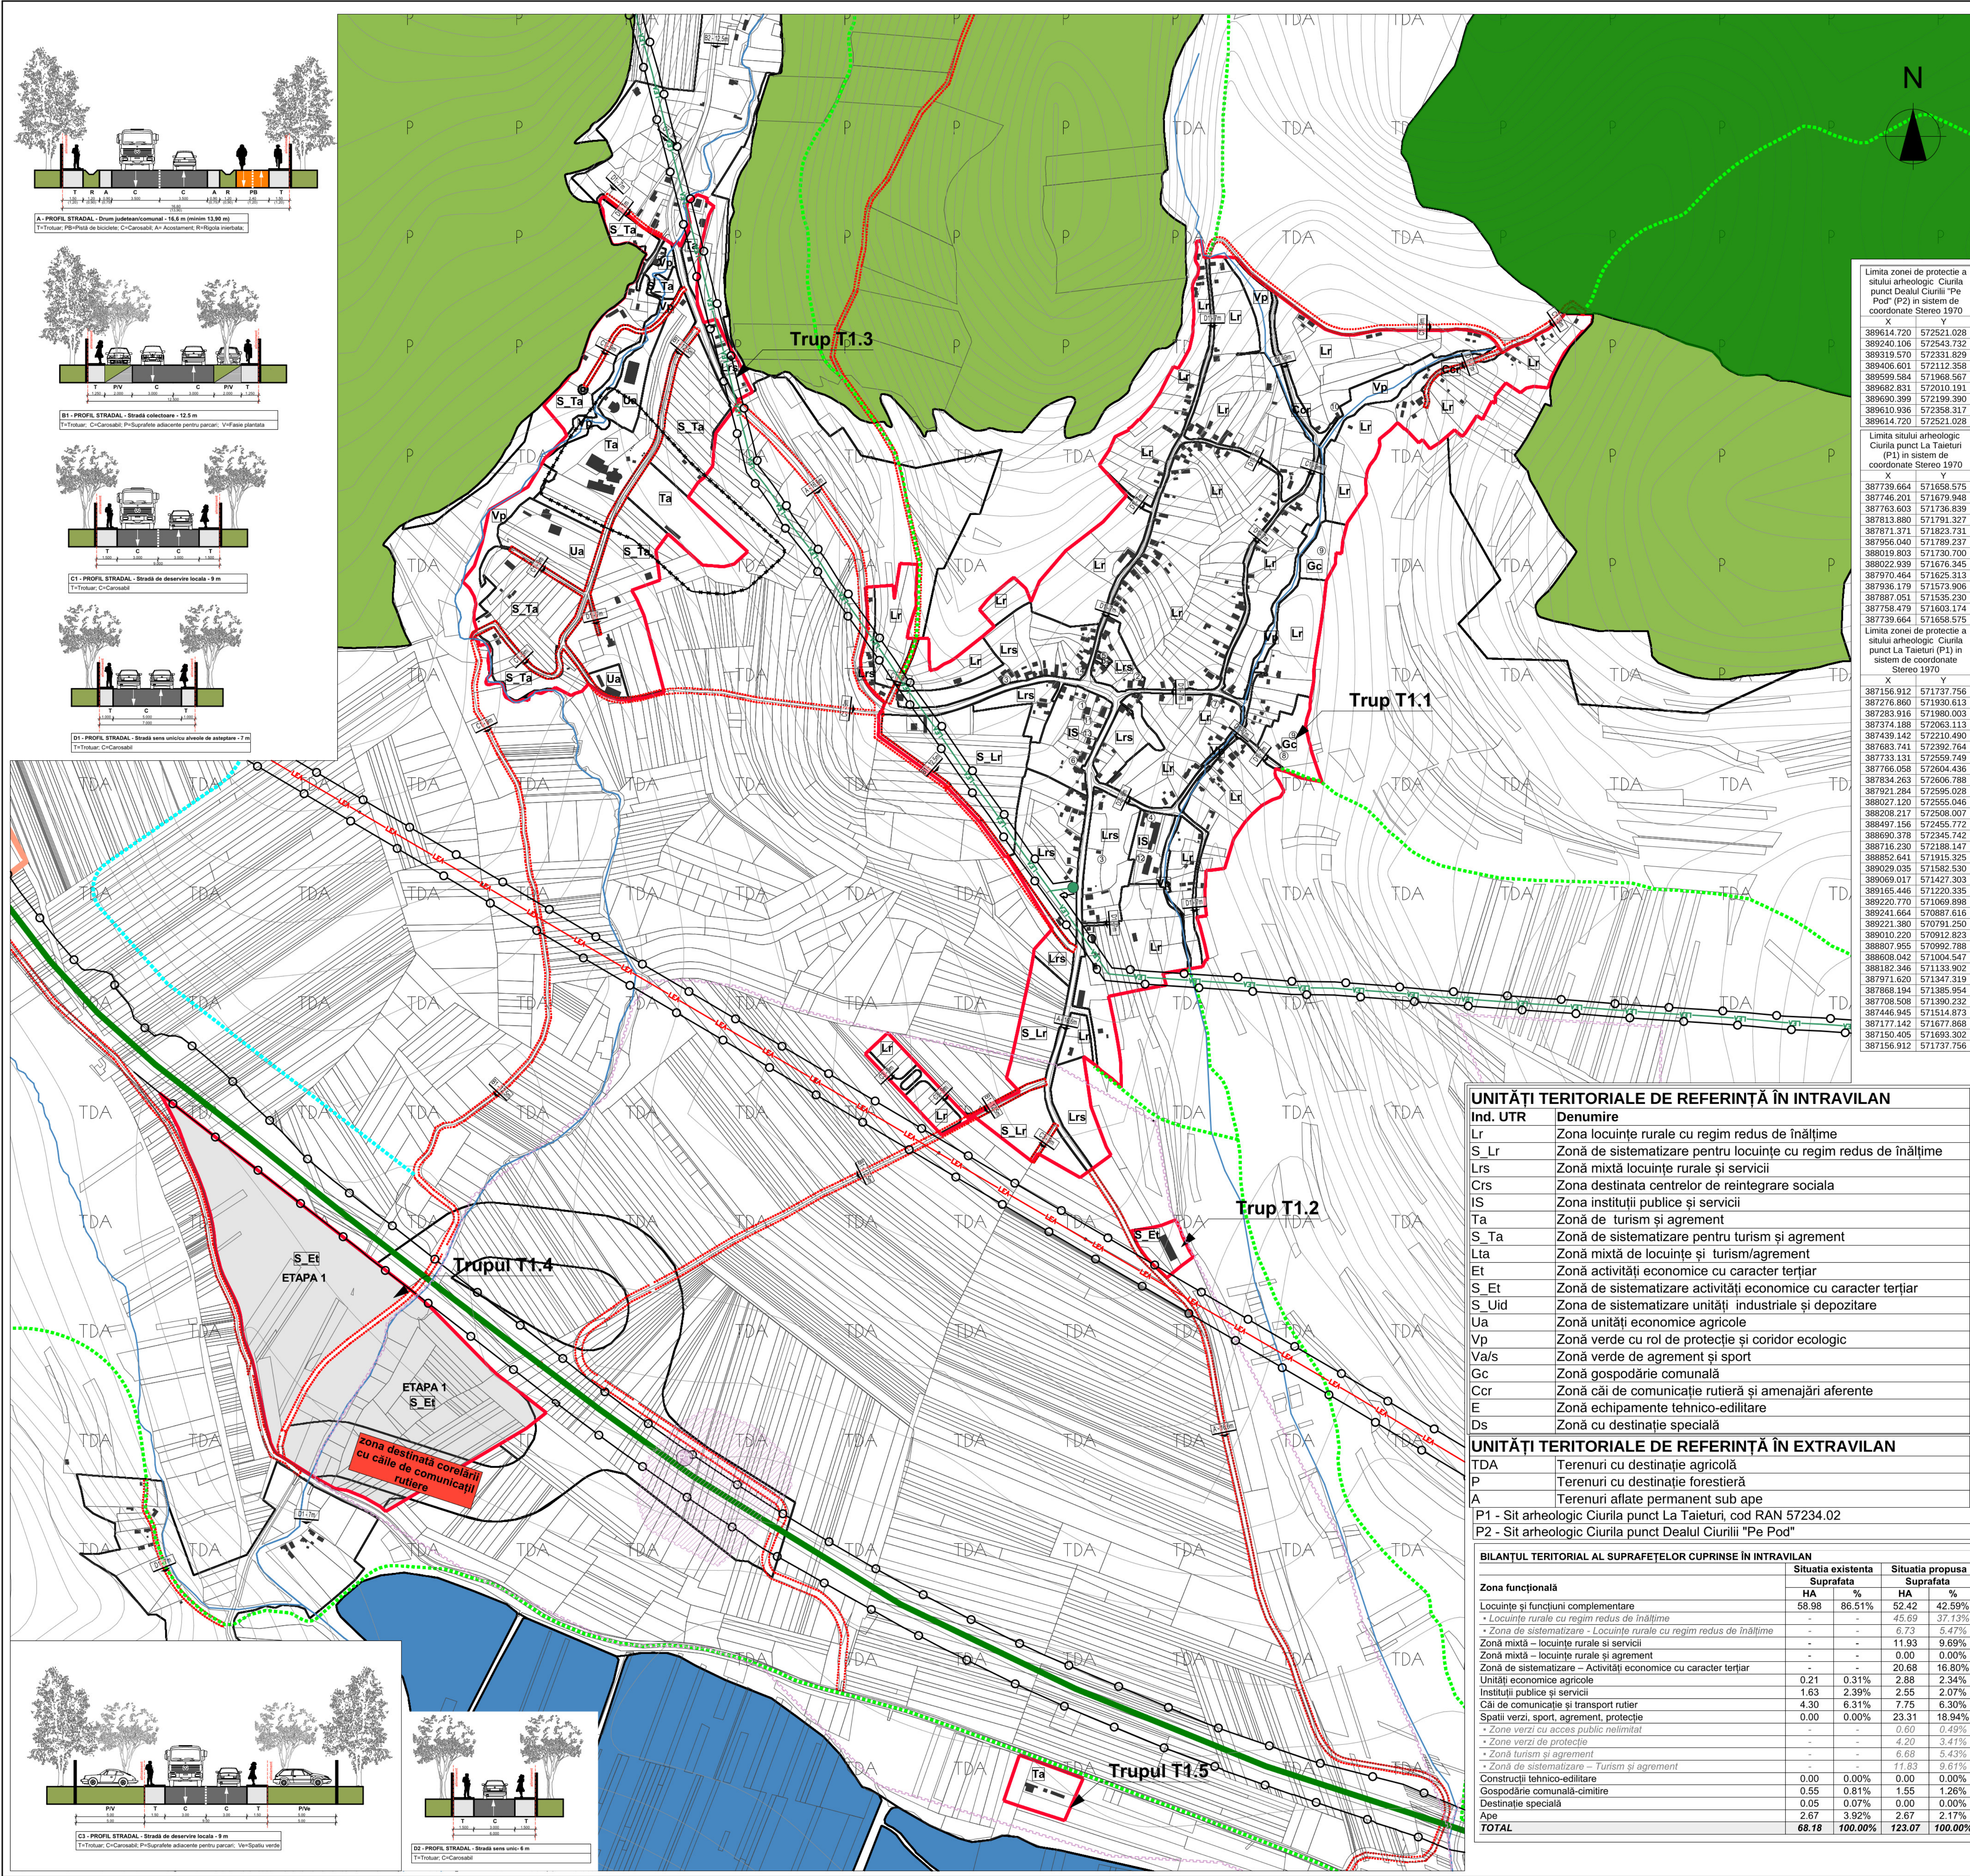

Obiective

1. Consiliul Local, remiza PSI și bibliotecă
2. Magazin mixt și bufet
3. Magazin mixt
4. Școala generală cls. I-VIII și grădiniță
5. Poliția
6. Dispensar uman
7. Dispensar veterinar
8. Biserica ortodoxă
9. Cimitir
10. Moara
11. Moara
12. Moara
13. Moara
14. Moara

LIMITE

Limita intravilan propus

Limita zonei centrale

Limita UTR

ZONE PROTEJATE ȘI ZONE DE PROTECȚIE

Sit de importanță comunitară Natura 2000

Zonă de protecție sanitară (surse de apă, immagazinări, stații de epurare ape uzate, ferme agrozootehnice, etc.)

Zonă de protecție față de construcții și culoare tehnice (stații electrice, linii de înaltă tensiune, rețele de gaze, etc.)

Sit arheologic

Zona de protecție față de obiective cu valoare de patrimoniu

DRUMURI

Autostrada

Drum județean

Străzi, ulițe, drumuri de exploatare

Străzi propuse spre modernizare/propuse

Traseu velo propus

Lucrări Tehnico-Edilitare

Linie electrică aeriană LEA 220kV

Linie electrică aeriană LEA 20kV

Punct de transformare

© Acest document este proprietatea firmei SC RAUM SRL și nu poate fi folosit, transmis sau reprodus, în orice formă, fără autorizația scrisă a firmei. Utilizarea sa trebuie să se conformeze cu legislația în vigoare. Documentul este valabil numai cu semnăturile și stempelul.

BENEFICIAR

COMUNA CIURILA
reprezentată prin primar Teodor Cristinel POPA

Adresa str. Principală, nr. 5, sat Ciurila, comuna Ciurila 407230

Contact primaria_ciurila@yahoo.com

PROIECTANT GENERAL

S.C. RAUM S.R.L.

Reprezentat prin: HORATIU RĂCĂȘAN

PROIECTANT DE SPECIALITATE - URBANISM

S.C. RAUM S.R.L.

Adresa Str. Octavian Goga, nr. 41, Cluj-Napoca

Contact raumoffice@gmail.com

SEF PROIECT arh. Horatiu RĂCĂȘAN, arh. Cezar Cîmpeanu

Desenat arh. Cezar Cîmpeanu

Verificat arh. Horatiu RĂCĂȘAN

PROIECT

Denumirea proiectului: PLAN URBANISTIC GENERAL COMUNA CIURILA, JUDEȚUL CLUJ

Proiect nr.: 131/2020

Denumire planșă: Reglementări UTR, reședința de comună Ciurila

Faza: PUG Scara: 1:5000 Data: 2023 Nr. planșă: 6.1

UNITĂȚI TERITORIALE DE REFERINȚĂ ÎN INTRAVILAN	
Ind. UTR	Denumire
Lr	Zona locuințe rurale cu regim redus de înălțime
S_Lr	Zonă de sistematizare pentru locuințe cu regim redus de înălțime
Lrs	Zonă mixtă locuințe rurale și servicii
Crs	Zona destinată centrelor de reintegrare sociala
IS	Zona instituții publice și servicii
Ta	Zonă de turism și agrement
S_Ta	Zonă de sistematizare pentru turism și agrement
Lta	Zonă mixtă de locuințe și turism/agrement
Et	Zonă activități economice cu caracter terțiar
S_Et	Zonă de sistematizare activități economice cu caracter terțiar
S_Uid	Zona de sistematizare unități industriale și depozitare
Ua	Zonă unități economice agricole
Vp	Zonă verde cu rol de protecție și coridor ecologic
Va/s	Zonă verde de agrement și sport
Gc	Zonă gospodărie comunală
Ccr	Zonă cai de comunicație rutieră și amenajări aferente
E	Zonă echipamente tehnico-edilitare
Ds	Zonă cu destinație specială

UNITĂȚI TERITORIALE DE REFERINȚĂ ÎN EXTRAVILAN	
TDA	Terenuri cu destinație agricolă
P	Terenuri cu destinație forestieră
A	Terenuri aflate permanent sub ape

P1 - Sit arheologic Ciurila punct La Taieturi, cod RAN 57234.02	
P2 - Sit arheologic Ciurila punct Dealul Ciurilii "Pe Pod"	

BILANȚUL TERITORIAL AL SUPRAFEȚELOR CUPRINSE ÎN INTRAVILAN					
Zona funcțională	Situația existentă		Situația propusă		
	HA	%	HA	%	
Locuințe și funcțiuni complementare	58.98	86.51%	52.42	42.59%	
• Locuințe rurale cu regim redus de înălțime	-	-	45.69	37.13%	
• Zona de sistematizare - Locuințe rurale cu regim redus de înălțime	-	-	6.73	5.47%	
Zonă mixtă - locuințe rurale și servicii	-	-	11.93	9.69%	
Zonă mixtă - locuințe rurale și agrement	-	-	0.00	0.00%	
Zonă de sistematizare - Activități economice cu caracter terțiar	-	-	20.68	16.80%	
Unități economice agricole	0.21	0.31%	2.88	2.34%	
Instituții publice și servicii	1.63	2.39%	2.55	2.07%	
Căi de comunicație și transport rutier	4.30	6.31%	7.75	6.30%	
Spatii verzi, sport, agrement, protecție	0.00	0.00%	23.31	18.94%	
• Zone verzi cu acces public nelimitat	-	-	0.60	0.49%	
• Zone verzi de protecție	-	-	4.20	3.41%	
• Zonă turism și agrement	-	-	6.68	5.43%	
• Zonă de sistematizare - Turism și agrement	-	-	11.83	9.61%	
Construcții tehnico-edilitare	0.00	0.00%	0.00	0.00%	
Gospodărie comunală-cimintire	0.55	0.81%	1.55	1.26%	
Destinație specială	0.05	0.07%	0.00	0.00%	
Ape	2.67	3.92%	2.67	2.17%	
TOTAL	68.18	100.00%	123.07	100.00%	