



Limita sitului arheologic Prunis punct La Fundoaia (P10) in sistem de coordonate Stereo 1970		Limita sitului arheologic Prunis castel fortificat (P11) in sistem de coordonate Stereo 1970		Limita sitului arheologic Prunis punct La Cruce (P12) in sistem de coordonate Stereo 1970	
X	Y	X	Y	X	Y
391081.998	571618.713	390283.129	572436.165	389617.903	570766.992
391137.288	571627.090	390264.809	572408.185	389685.889	570894.382
391224.410	571769.501	390259.435	572380.773	389526.155	570948.760
390964.718	571937.044	390259.726	572372.359	389473.392	570990.072
390832.359	571994.009	390279.225	572326.641	389392.981	571071.533
390760.316	571918.615	390291.569	572315.223	389288.783	571110.124
390607.852	571756.098	390306.028	572306.638	389254.193	570883.020
390542.510	571667.300	390321.961	572301.265	389251.840	570876.427
390589.422	571553.371	390412.390	572346.583	389404.361	570696.447
390835.710	571513.161	390419.399	572379.284	389576.051	570694.095
390968.069	571533.266	390398.663	572433.061	389617.903	570766.992
391081.998	571618.713	390394.748	572437.085	Limita zonei de protecție a sitului arheologic Prunis punct La Cruce (P12) in sistem de coordonate Stereo 1970	
Limita zonei de protecție a sitului arheologic Prunis punct La Fundoaia (P10) in sistem de coordonate Stereo 1970		390390.560	572440.824		
		390368.922	572453.672		
		390363.635	572455.559		
X	Y	X	Y	X	Y
390485.322	572280.641	390338.752	572459.312	390381.097	570493.448
390486.812	572233.729	390283.129	572436.165	390331.014	570797.579
390459.260	572180.115	Limita zonei de protecție a sitului arheologic Prunis castel fortificat (P11) in sistem de coordonate Stereo 1970		390316.903	571021.011
390431.709	572128.735			390236.938	571256.202
390407.136	572057.995			389797.107	571331.722
390400.434	572022.252			389616.543	571406.414
390421.838	571896.639	X	Y	389572.655	571326.951
390427.985	571874.628	390108.454	572213.513	389473.428	571369.886
390477.876	571861.969	390120.028	572196.976	389364.661	571258.971
390495.747	571609.538	390104.354	572146.009	389244.444	571101.068
390505.428	571396.945	390195.696	572105.704	389223.590	571044.951
390478.464	571129.497	390249.310	572047.623	389241.664	570887.616
390828.785	570989.071	390293.988	572109.055	389217.252	570771.664
390846.263	571053.518	390327.497	572049.857	389248.022	570744.472
391158.034	571006.382	390577.561	571991.574	389245.160	570671.961
391197.885	571330.182	390607.171	572176.773	389297.460	570661.536
391301.825	571493.254	390638.594	572253.001	389473.190	570624.256
391469.917	571911.488	390532.107	572311.544	389497.042	570628.072
391389.496	571986.882	390506.831	572307.558	389605.810	570611.852
391372.742	572040.496	390538.601	572603.586	389678.321	570621.393
391326.524	572180.237	390268.532	572613.708	389764.191	570601.357
391161.637	572278.407	390148.546	572535.023	389830.023	570575.597
391126.453	572345.424	390081.767	572453.914	389915.893	570533.616
390856.709	572332.021	390041.557	572395.833	389976.955	570471.600
390811.473	572303.538	390145.595	572303.781	390420.514	570304.426
390766.912	572290.135	390108.454	572213.513	390381.097	570493.448
390643.557	572336.675				
390595.901	572369.438				
390517.280	572351.516				
390471.174	572334.999				
390485.322	572280.641				

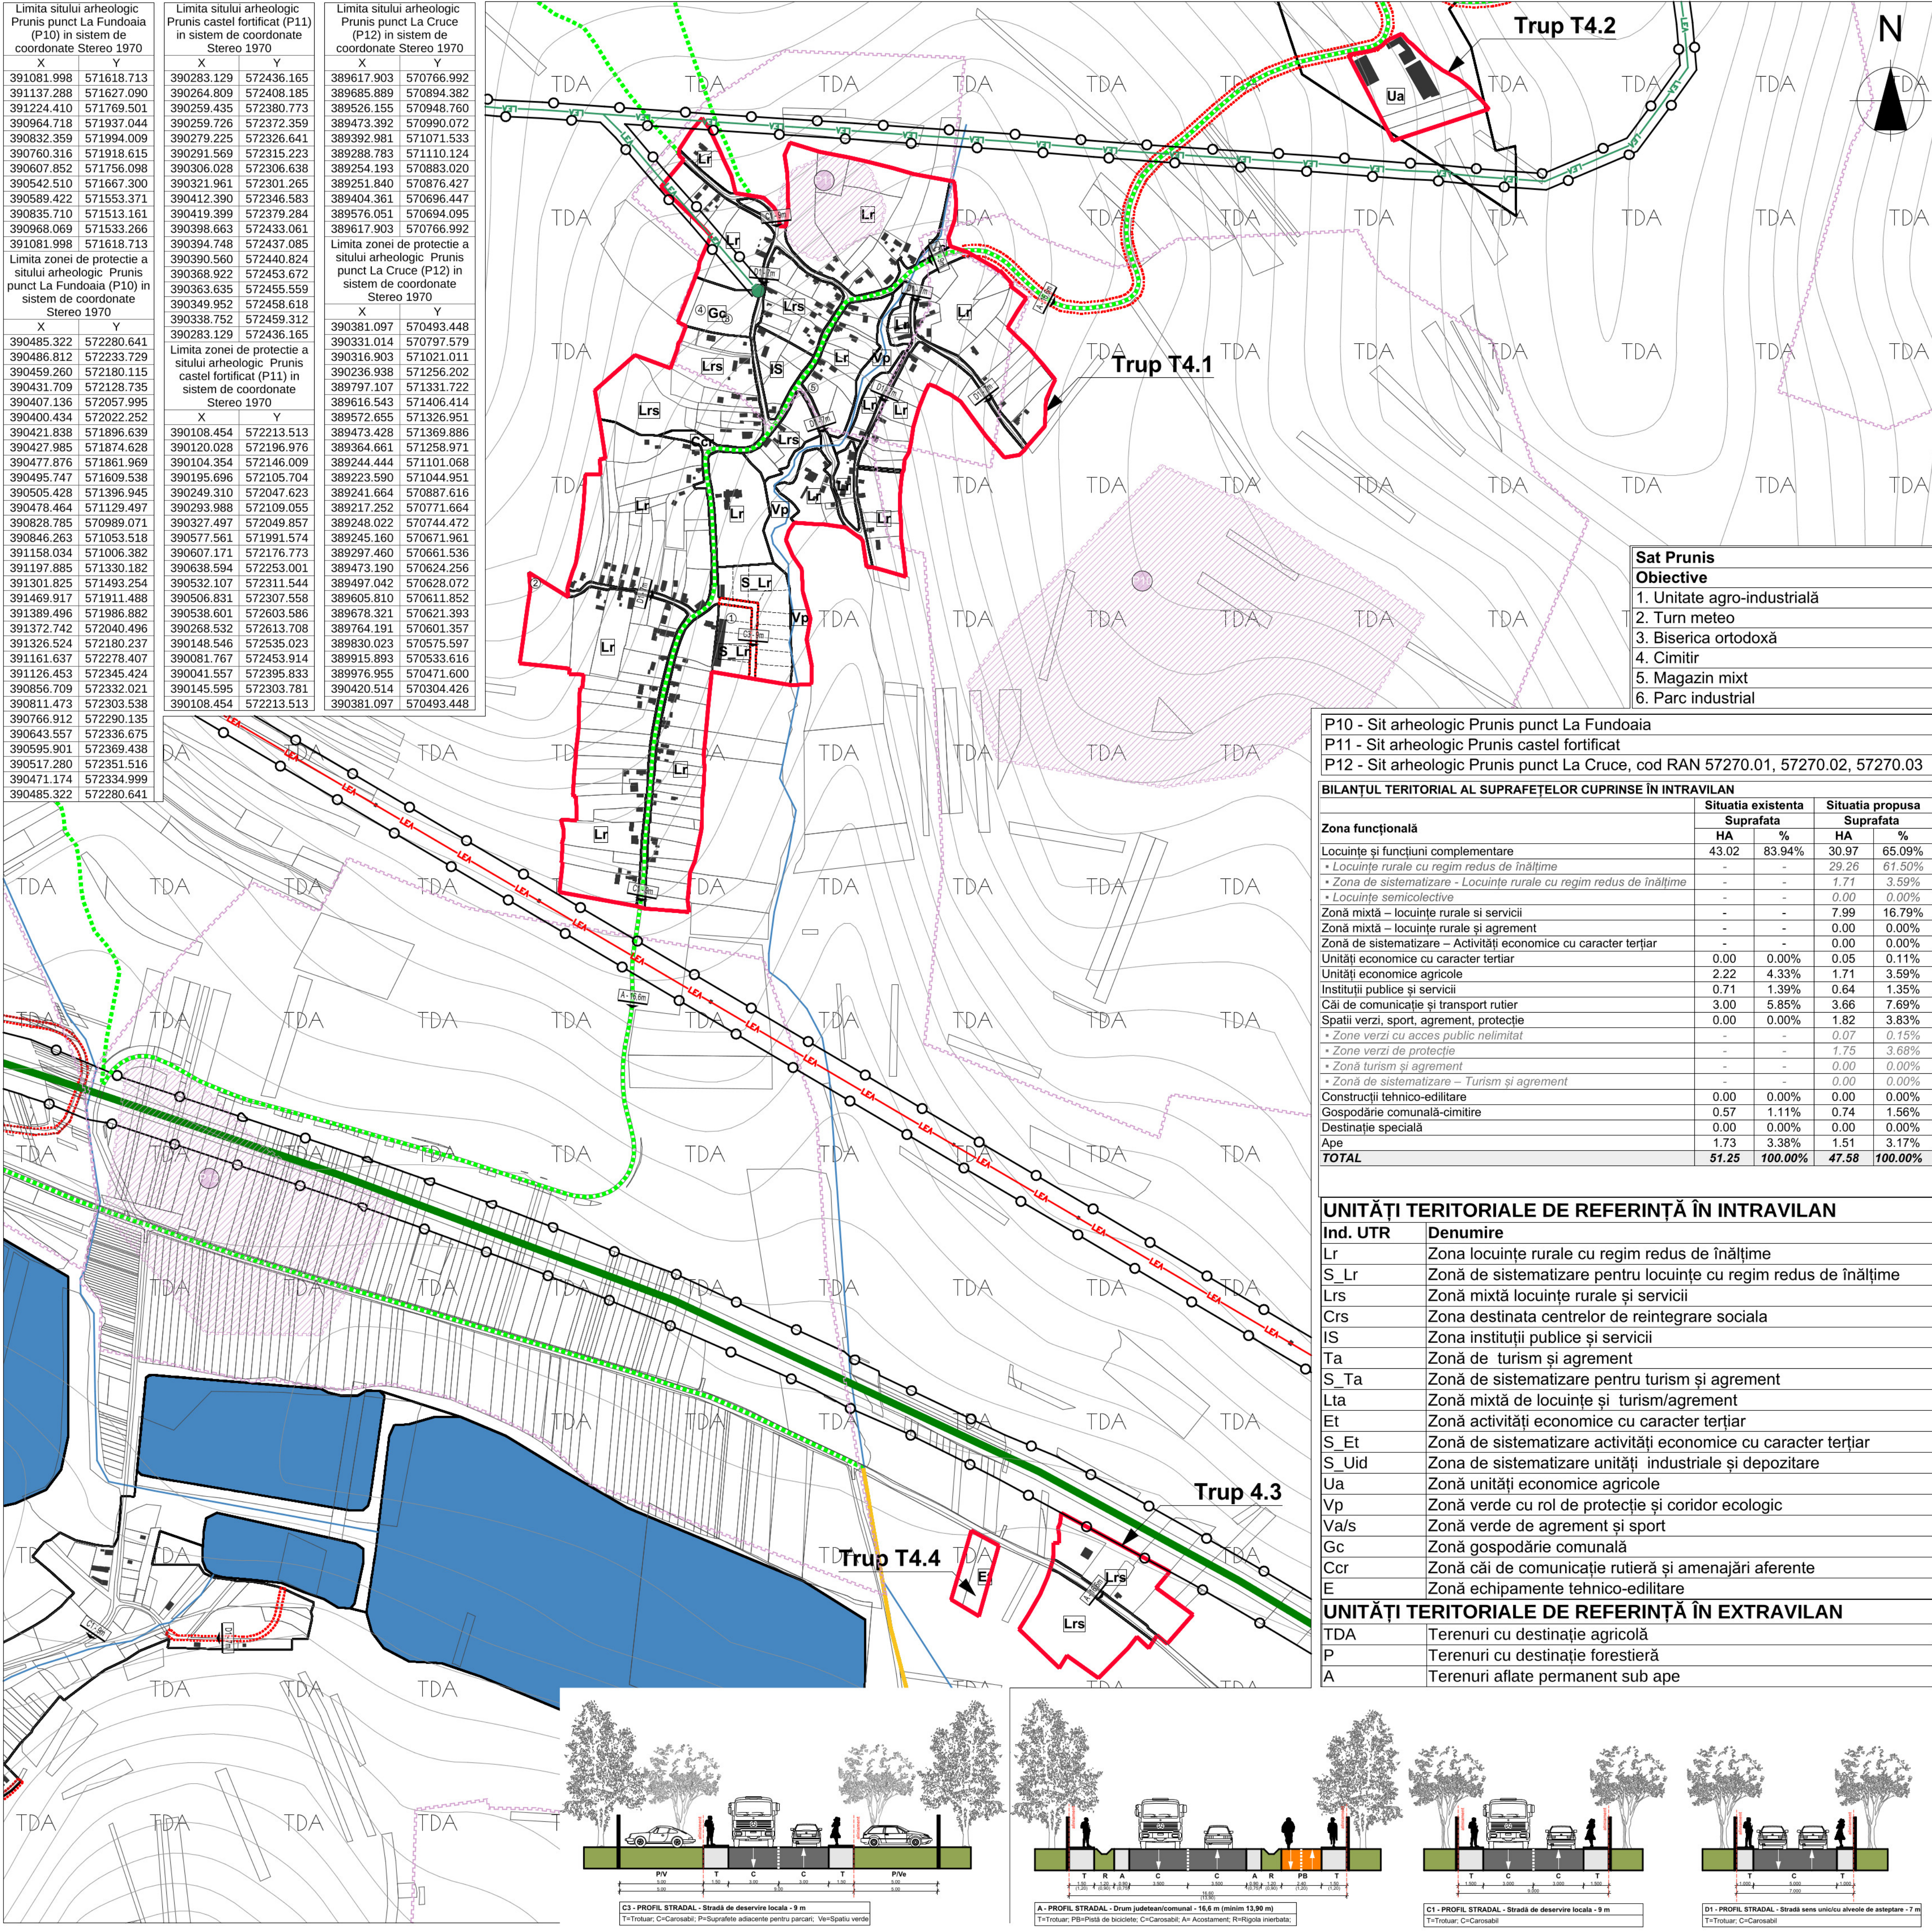


LEGENDĂ


LIMITE

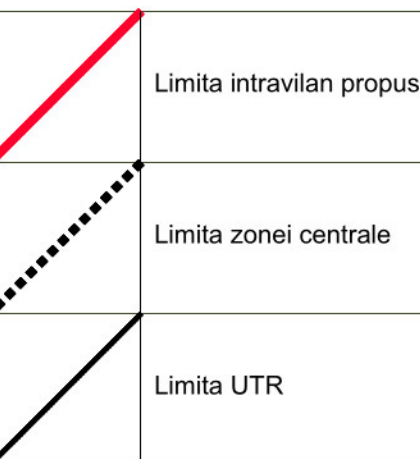


ZONE PROTEJATE ȘI ZONE DE PROTECȚIE

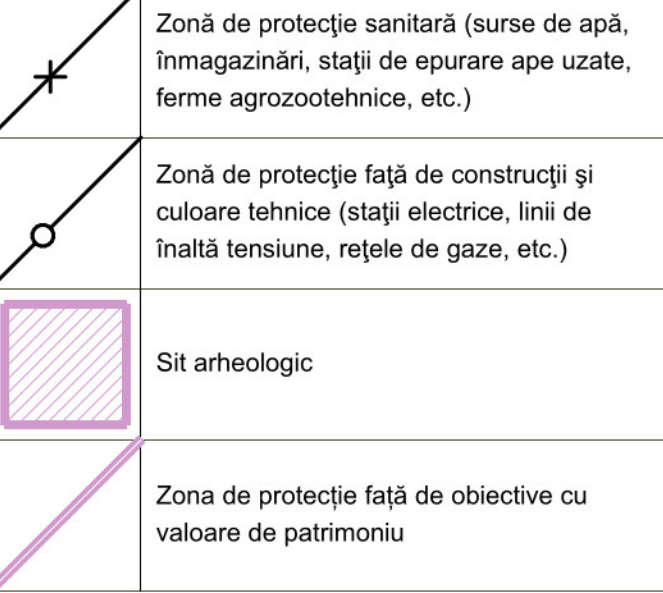

DRUMURI

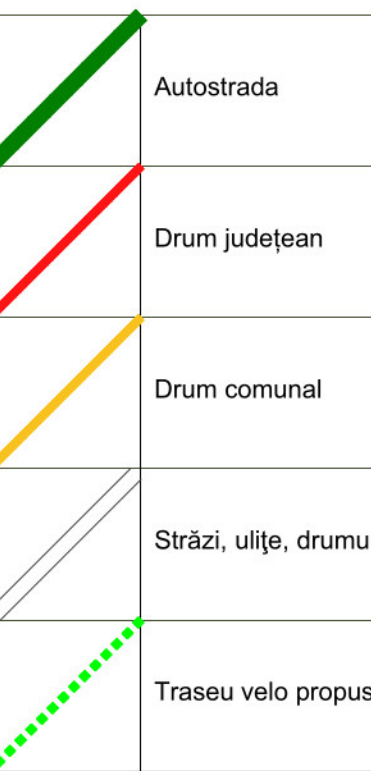

LUCRĂRI TEHNICO-EDILITARE

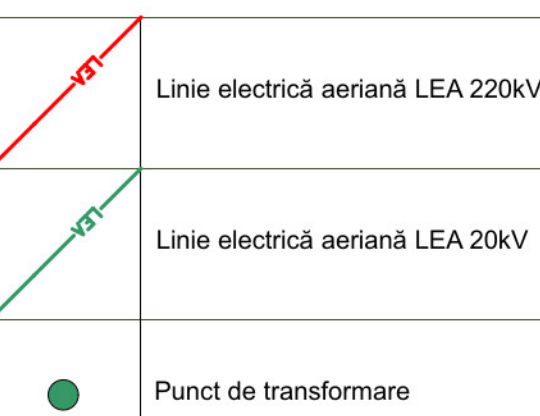

© Acest document este proprietatea firmei SC RAUM SRL si nu poate fi folosit, transmis sau reprodus, total sau partial, fara autorizarea expresa si scrisa. Utilizarea sa trebuie sa fie conforma cu cele pentru care a fost elaborat. Documentul este valabil numai cu semnatura si stampila proiectantilor si original.

BENEFICIAR

COMUNA CIURILA
reprezentată prin primar Teodor Cristinel POPA
Adresa str. Principală, nr. 5, sat Ciurila, comuna Ciurila 407230

Contact primaria_ciurila@yahoo.com

PROIECTANT GENERAL

S.C. RAUM S.R.L

Reprezentată prin: HORATIU RĂCĂȘAN

PROIECTANT DE SPECIALITATE - URBANISM

S.C. RAUM S.R.L

Adresa Str. Octavian Goga, nr. 41, Cluj-Napoca

Contact raumoffice@gmail.com

SEF PROIECT arh. Horatiu RĂCĂȘAN

Proiectat arh. Horatiu RĂCĂȘAN, arh. Cezar Cîmpeanu

Desenat arh. Cezar Cîmpeanu

Verificat arh. Horatiu RĂCĂȘAN

PROIECT

Denumirea proiectului:

PLAN URBANISTIC GENERAL COMUNA CIURILA, JUD. CLUJ

Proiect nr.: 131/2020

Denumire planșă:

Reglementări UTR, loc. Pruniș

Faza:

PUG

Scara:

1:5000

Data:

2023

Nr. planșă:

6.4

P10 - Sit arheologic Prunis punct La Fundoaia
P11 - Sit arheologic Prunis castel fortificat
P12 - Sit arheologic Prunis punct La Cruce, cod RAN 57270.01, 57270.02, 57270.03

BILANȚUL TERITORIAL AL SUPRAFEȚELOR CUPRINSE ÎN INTRAVILAN

Zona funcțională	Situatia existenta		Situatia propusa	
	Suprafata		Suprafata	
	HA	%	HA	%
Locuințe și funcțiuni complementare	43.02	83.94%	30.97	65.09%
• Locuințe rurale cu regim redus de înălțime	-	-	29.26	61.50%
• Zona de sistematizare - Locuințe rurale cu regim redus de înălțime	-	-	1.71	3.59%
• Locuințe semicollective	-	-	0.00	0.00%
Zonă mixtă - locuințe rurale si servicii	-	-	7.99	16.79%
Zonă mixtă - locuințe rurale și agrement	-	-	0.00	0.00%
Zonă de sistematizare - Activități economice cu caracter terțiar	-	-	0.00	0.00%
Unități economice cu caracter terțiar	0.00	0.00%	0.05	0.11%
Unități economice agricole	2.22	4.33%	1.71	3.59%
Instituții publice și servicii	0.71	1.39%	0.64	1.35%
Căi de comunicație și transport rutier	3.00	5.85%	3.66	7.69%
Spatii verzi, sport, agrement, protecție	0.00	0.00%	1.82	3.83%
• Zone verzi cu acces public nelimitat	-	-	0.07	0.15%
• Zone verzi de protecție	-	-	1.75	3.68%
• Zonă turism și agrement	-	-	0.00	0.00%
• Zonă de sistematizare - Turism și agrement	-	-	0.00	0.00%
Construcții tehnico-edilitare	0.00	0.00%	0.00	0.00%
Gospodărie comunală-cimintire	0.57	1.11%	0.74	1.56%
Destinație specială	0.00	0.00%	0.00	0.00%
Ape	1.73	3.38%	1.51	3.17%
TOTAL	51.25	100.00%	47.58	100.00%

UNITĂȚI TERITORIALE DE REFERINȚĂ ÎN INTRAVILAN

Ind. UTR	Denumire
Lr	Zona locuințe rurale cu regim redus de înălțime
S_Lr	Zonă de sistematizare pentru locuințe cu regim redus de înălțime
Lrs	Zonă mixtă locuințe rurale și servicii
Crs	Zona destinata centrelor de reintegrare sociala
IS	Zona instituții publice și servicii
Ta	Zonă de turism și agrement
S_Ta	Zonă de sistematizare pentru turism și agrement
Lta	Zonă mixtă de locuințe și turism/agrement
Et	Zonă activități economice cu caracter terțiar
S_Et	Zonă de sistematizare activități economice cu caracter terțiar
U_Uid	Zona de sistematizare unități industriale și depozitare
Ua	Zonă unități economice agricole
Vp	Zonă verde cu rol de protecție și coridor ecologic
Va/s	Zonă verde de agrement și sport
Gc	Zonă gospodărie comunală
Ccr	Zonă căi de comunicație rutieră și amenajări aferente
E	Zonă echipamente tehnico-edilitare

UNITĂȚI TERITORIALE DE REFERINȚĂ ÎN EXTRAVILAN

TDA	Terenuri cu destinație agricolă
P	Terenuri cu destinație forestieră
A	Terenuri aflate permanent sub ape

