


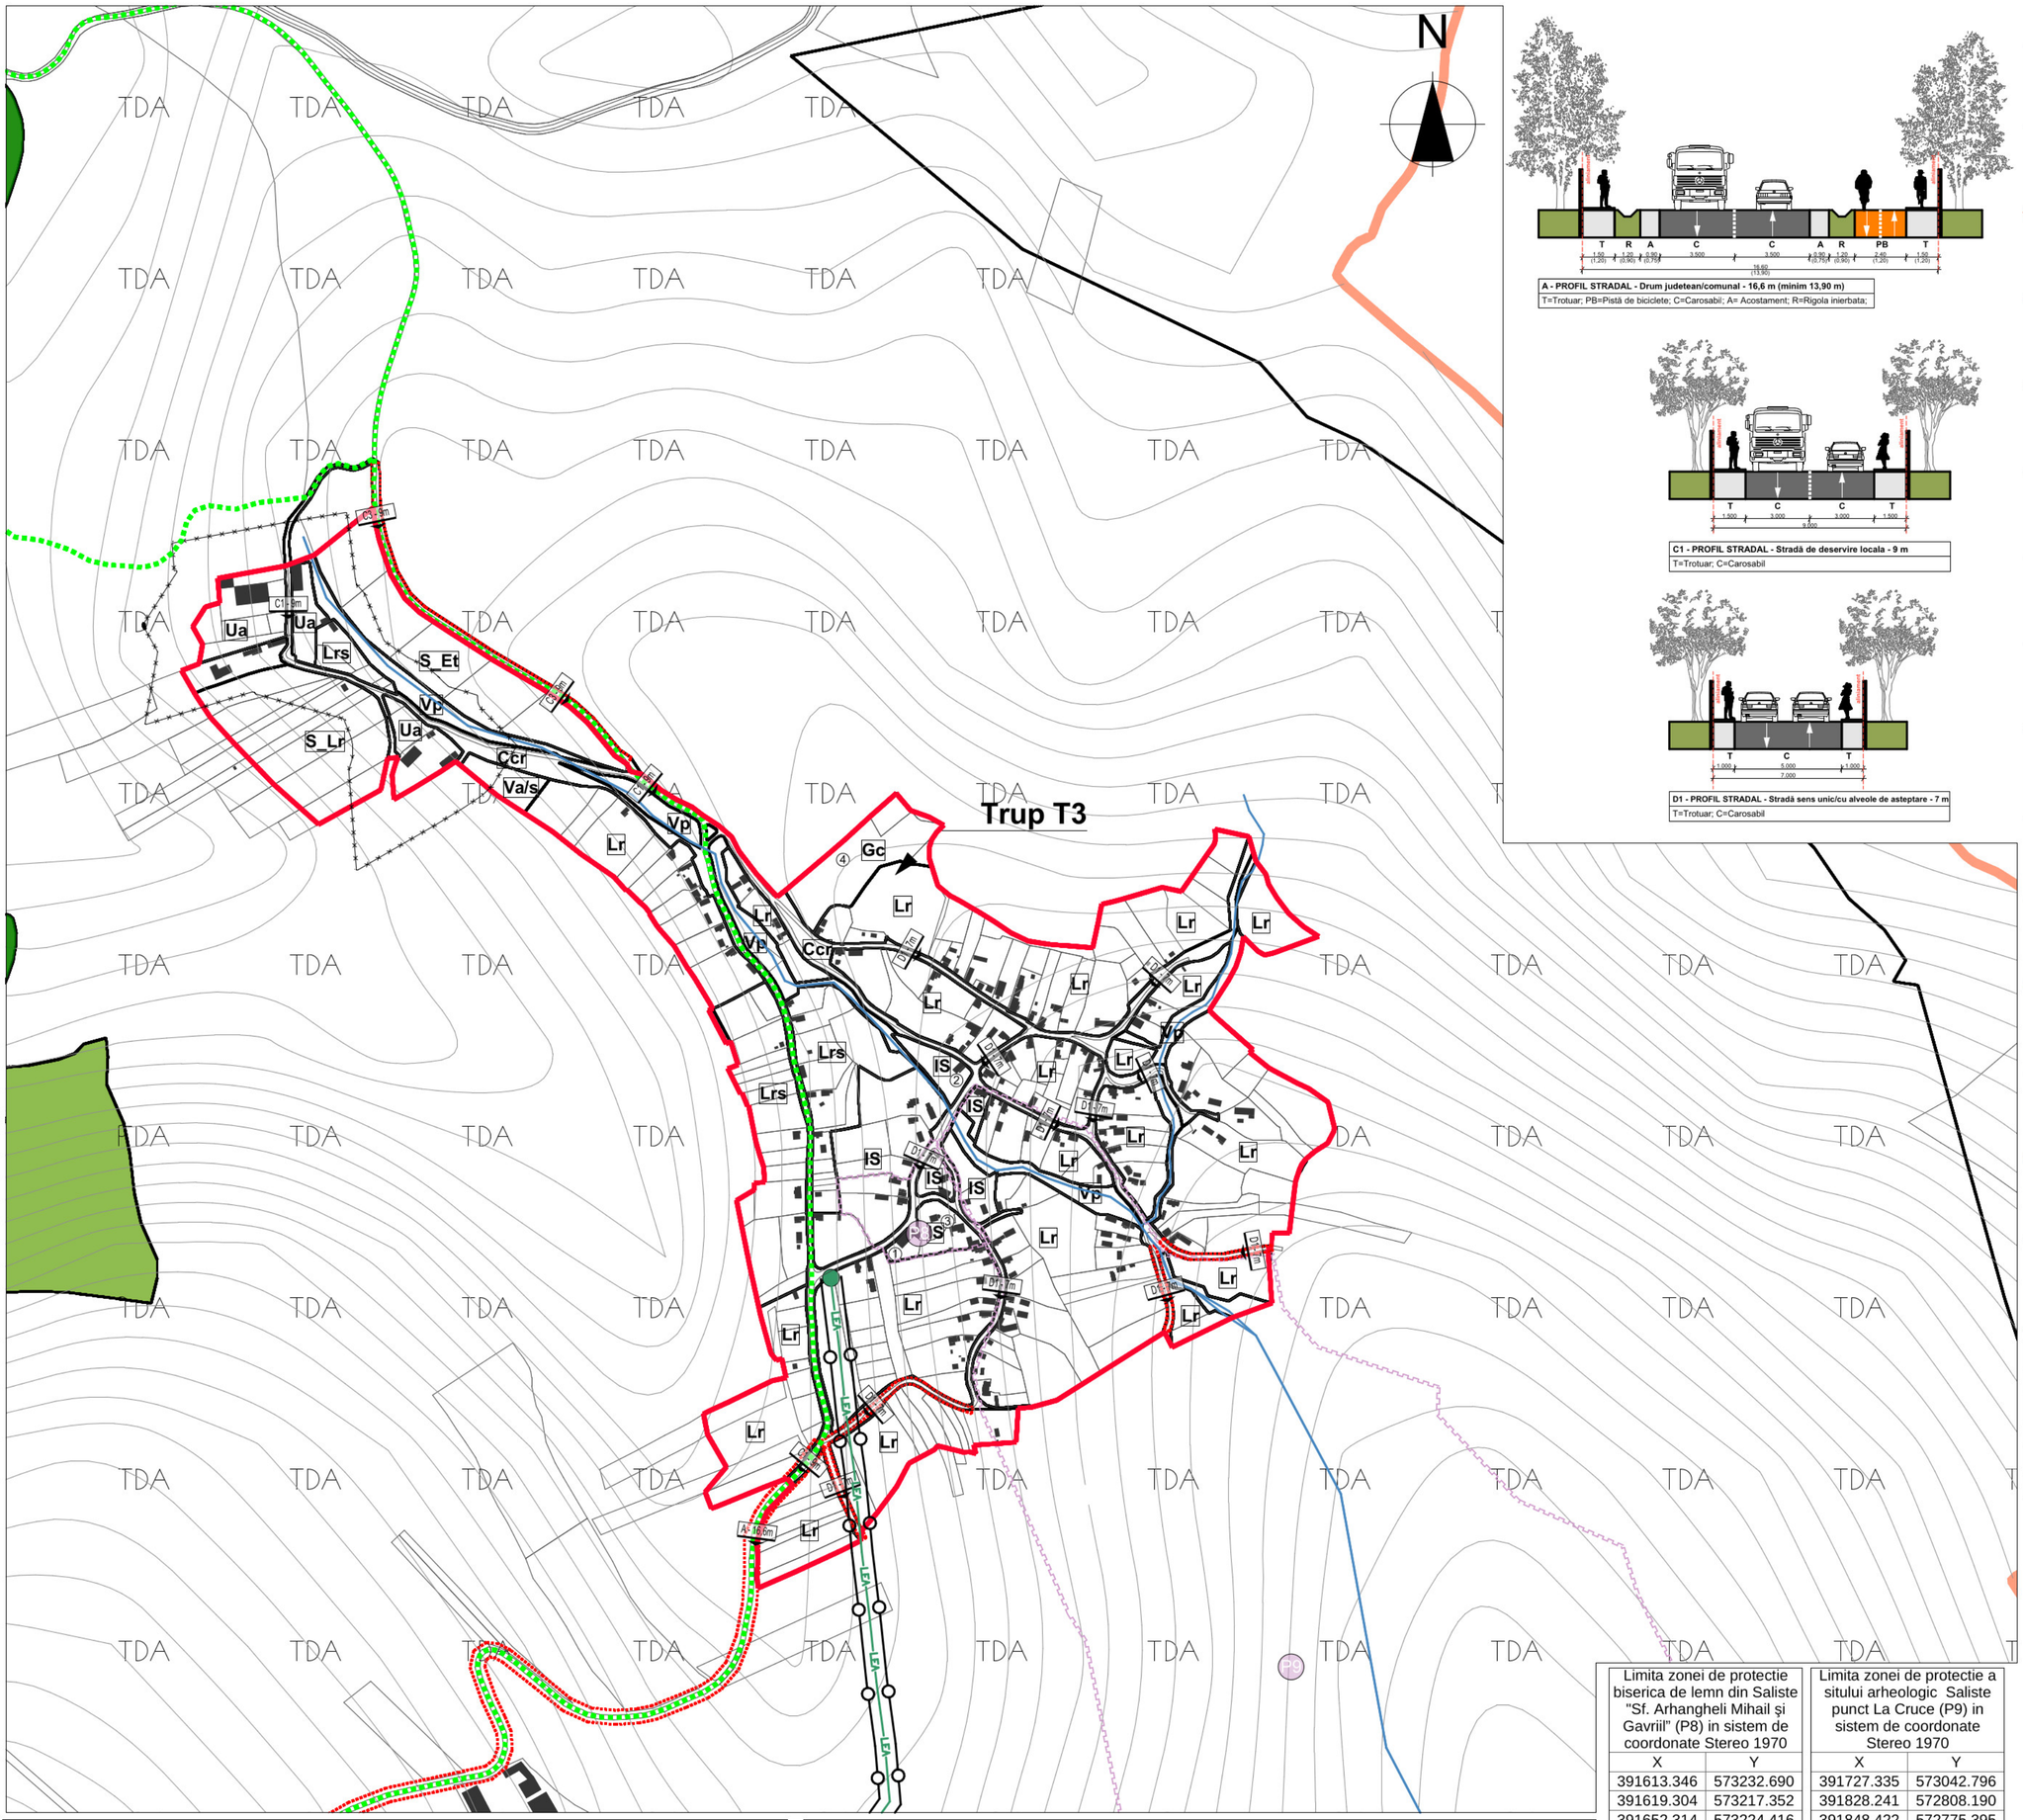









## LEGENDĂ

### LIMITE

- Limita UAT Ciurila
- Limita intravilan propus
- Limita zonei centrale
- Limita UTR

### ZONE PROTEJATE ŞI ZONE DE PROTECŢIE

- Zonă de protecţie sanitară (surse de apă, înmagazinări, staţii de epurare ape uzate, ferme agrozootehnice, etc.)
- Zonă de protecţie faţă de construcţii şi culoare tehnice (staţii electrice, linii de înaltă tensiune, reţele de gaze, etc.)
- Obiectiv cu valoare de patrimoniu înscris în Lista monumentelor istorice din 2015
- Sit arheologic
- Zona de protecţie faţă de obiective cu valoare de patrimoniu

### DRUMURI

- Drum comunal
- Străzi, uliţe, drumuri de exploatare
- Traseu velo propus

| Sat Saliste |
|---|
| **Obiective** |
| 1. Școala generală cls. I-IV |
| 2. Magazin mixt |
| 3. Biserica ortodoxă |
| 4. Cimitir |

P8 - Biserica de lemn din Saliste "Sf. Arhangheli Mihail şi Gavriil", cod LMI CJ-II-m-B-07748

P9 - Sit arheologic Saliste punct La Cruce

**BILANŢUL TERITORIAL AL SUPRAFEŢELOR CUPRINSE ÎN INTRAVILAN**

| Zona funcțională | Situatia existenta Suprafata HA | % | Situatia propusa Suprafata HA | % |
|---|---|---|---|---|
| Locuințe și funcțiuni complementare | 31.66 | 80.58% | 34.81 | 65.92% |
| *▪ Locuințe rurale cu regim redus de înălțime* | - | - | *28.96* | *54.84%* |
| *▪ Zona de sistematizare - Locuințe rurale* | - | - | *5.85* | *11.08%* |
| Zonă mixtă – locuințe rurale si servicii | - | - | 4.74 | 8.98% |
| Zonă mixtă – locuințe rurale și agrement | - | - | 0.00 | 0.00% |
| Zonă de sistematizare – Activități economice cu caracter terțiar | - | - | 0.00 | 0.00% |
| Unități economice agricole | 0.66 | 1.68% | 1.69 | 3.20% |
| Unități economice cu caracter tertiar | - | - | *2.70* | *5.11%* |
| Instituții publice și servicii | 0.41 | 1.04% | 3.33 | 6.31% |
| Căi de comunicație și transport rutier | 3.91 | 9.95% | 8.67 | 16.42% |
| Spatii verzi, sport, agrement, protecție | 0.00 | 0.00% | 3.19 | 6.04% |
| *▪ Zone verzi cu acces public nelimitat* | - | - | *0.32* | *0.61%* |
| *▪ Zone verzi de protecție* | - | - | *2.87* | *5.43%* |
| *▪ Zonă turism și agrement* | - | - | *0.00* | *0.00%* |
| *▪ Zonă de sistematizare – Turism și agrement* | - | - | *0.00* | *0.00%* |
| Construcții tehnico-edilitare | 0.00 | 0.00% | 0.00 | 0.00% |
| Gospodărie comunală-cimitire | 1.10 | 2.80% | 1.12 | 2.12% |
| Destinație specială | 0.00 | 0.00% | 0.00 | 0.00% |
| Ape | 1.54 | 3.92% | 1.57 | 2.97% |
| ***TOTAL*** | ***39.29*** | ***100.00%*** | ***52.81*** | ***100.00%*** |

**UNITĂȚI TERITORIALE DE REFERINȚĂ ÎN INTRAVILAN**

| Ind. UTR | Denumire |
|---|---|
| Lr | Zona locuințe rurale cu regim redus de înălțime |
| S_Lr | Zonă de sistematizare pentru locuințe cu regim redus de înălțime |
| Lrs | Zonă mixtă locuințe rurale și servicii |
| Crs | Zona destinata centrelor de reintegrare sociala |
| IS | Zona instituții publice și servicii |
| Ta | Zonă de turism și agrement |
| S_Ta | Zonă de sistematizare pentru turism și agrement |
| Lta | Zonă mixtă de locuințe și turism/agrement |
| Et | Zonă activități economice cu caracter terțiar |
| S_Et | Zonă de sistematizare activități economice cu caracter terțiar |
| S_Uid | Zona de sistematizare unități industriale și depozitare |
| Ua | Zonă unități economice agricole |
| Vp | Zonă verde cu rol de protecție și coridor ecologic |
| Va/s | Zonă verde de agrement și sport |
| Gc | Zonă gospodărie comunală |
| Ccr | Zonă căi de comunicație rutieră și amenajări aferente |
| E | Zonă echipamente tehnico-edilitare |

**UNITĂȚI TERITORIALE DE REFERINȚĂ ÎN EXTRAVILAN**

| | |
|---|---|
| TDA | Terenuri cu destinație agricolă |
| P | Terenuri cu destinație forestieră |
| A | Terenuri aflate permanent sub ape |

Limita zonei de protectie biserica de lemn din Saliste "Sf. Arhangheli Mihail și Gavriil" (P8) in sistem de coordonate Stereo 1970

| X | Y |
|---|---|
| 391613.346 | 573232.690 |
| 391619.304 | 573217.352 |
| 391652.314 | 573224.416 |
| 391675.832 | 573227.817 |
| 391686.168 | 573230.736 |
| 391709.976 | 573233.244 |
| 391730.802 | 573238.964 |
| 391735.795 | 573241.851 |
| 391727.034 | 573257.003 |
| 391723.307 | 573260.191 |
| 391713.793 | 573266.616 |
| 391707.466 | 573273.482 |
| 391705.063 | 573277.552 |
| 391702.317 | 573284.860 |
| 391701.238 | 573292.804 |
| 391700.649 | 573313.697 |
| 391697.658 | 573322.721 |
| 391691.874 | 573333.104 |
| 391683.141 | 573345.378 |
| 391669.553 | 573361.918 |
| 391659.809 | 573346.355 |
| 391651.483 | 573334.846 |
| 391647.342 | 573326.694 |
| 391641.457 | 573313.093 |
| 391621.491 | 573318.150 |
| 391622.363 | 573320.809 |
| 391613.382 | 573320.983 |
| 391558.542 | 573314.793 |
| 391560.035 | 573302.096 |
| 391560.503 | 573298.118 |
| 391562.530 | 573274.927 |
| 391577.047 | 573272.507 |
| 391583.062 | 573266.492 |
| 391599.629 | 573235.714 |
| 391613.346 | 573232.690 |

Limita zonei de protectie a sitului arheologic Saliste punct La Cruce (P9) in sistem de coordonate Stereo 1970

| X | Y |
|---|---|
| 391727.335 | 573042.796 |
| 391828.241 | 572808.190 |
| 391848.422 | 572775.395 |
| 391896.353 | 572535.743 |
| 391863.558 | 572472.677 |
| 391755.084 | 572104.370 |
| 391916.534 | 572048.872 |
| 392075.461 | 572111.938 |
| 392075.461 | 572177.527 |
| 392332.771 | 572286.001 |
| 392325.203 | 572344.022 |
| 392431.155 | 572386.907 |
| 392544.674 | 572636.649 |
| 392529.538 | 572682.057 |
| 392557.287 | 572697.193 |
| 392491.698 | 572830.894 |
| 392474.040 | 572886.392 |
| 392352.953 | 572939.368 |
| 392258.493 | 573039.993 |
| 392259.334 | 573071.947 |
| 392118.066 | 573119.036 |
| 392077.703 | 573165.005 |
| 392065.904 | 573227.705 |
| 392002.362 | 573220.093 |
| 391942.838 | 573225.703 |
| 391849.624 | 573373.592 |
| 391719.183 | 573424.088 |
| 391672.429 | 573350.425 |
| 391731.603 | 573239.603 |
| 391753.614 | 573189.360 |
| 391717.525 | 573086.803 |
| 391727.335 | 573042.796 |

© Acest document este proprietatea firmei SC RAUM SRL si nu poate fi folosit, transmis sau reprodus, total sau partial, fara autorizarea expresa si scrisa. Utilizarea sa trebuie sa fie conforma celei pentru care a fost elaborat. Documentul este valabil numai cu semnaturile si stampila proiectantilor in original.

**BENEFICIAR**

**COMUNA CIURILA**
reprezentată prin primar Teodor Cristinel POPA

| | |
|---|---|
| Adresa | str. Principală, nr. 5, sat Ciurila, comuna Ciurila 407230 |
| Contact | primaria_ciurila@yahoo.com |

**PROIECTANT GENERAL**

**S.C. RAUM S.R.L**

Reprezentată prin: **HORAȚIU RĂCĂȘAN**

**PROIECTANT DE SPECIALITATE - URBANISM**

**S.C. RAUM S.R.L**

| | |
|---|---|
| Adresa | Str. Octavian Goga, nr. 41, Cluj-Napoca |
| Contact | raumoffice@gmail.com |

| | |
|---|---|
| SEF PROIECT | **arh. Horatiu RĂCĂȘAN** |
| Proiectat | **arh. Horatiu RĂCĂȘAN, arh. Cezar Cîmpeanu** |
| Desenat | **arh. Cezar Cîmpeanu** |
| Verificat | **arh. Horatiu RĂCĂȘAN** |

**PROIECT**

Denumirea proiectului:
**PLAN URBANISTIC GENERAL COMUNA CIURILA, JUD. CLUJ**

Proiect nr.: 131/2020

Denumire planșă:
**Reglementări UTR, loc. Sălişte**

| Faza: | Scara: | Data: | Nr. planșă: |
|---|---|---|---|
| PUG | 1:5000 | 2023 | 6.3 |