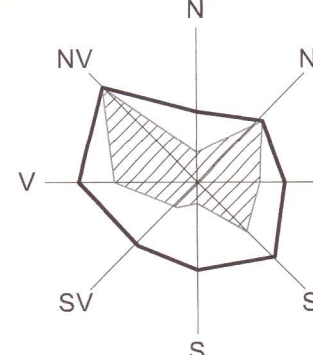


6.1 Reglementări urbanistice - UTR, reședința de comună Jucu de Sus

 


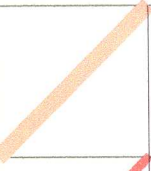
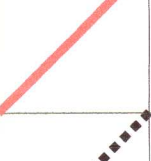
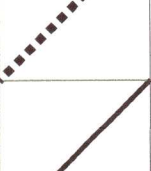
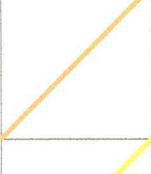
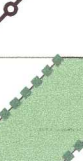
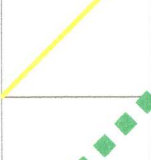
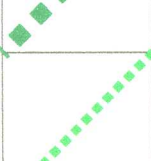
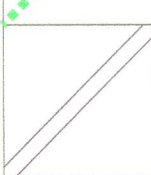
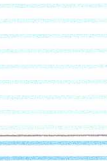
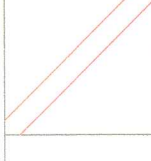
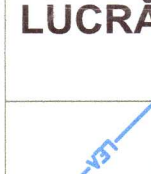
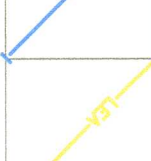
BILANTUL TERITORIAL AL SUPRAFELELOR CUPRINSE IN STRAVILAN		Situatia existenta		Situatia propusa	
Zona functionala		Hektare	%	Hektare	%
Locuinte si functii complementare		188.10	61.05%	300.66	68.41%
- Locuinte rurale		-	-	236.63	65.33%
- Locuinte colective		-	-	2.33	0.57%
- Locuinte semicollective		-	-	11.70	2.61%
Zona mica - servicii si servicii		-	-	15.24	3.37%
- Industriale si depozitare		41.62	13.51%	0.58	0.13%
- Piere industriale		-	-	0.00	0.00%
- Piere comerciale		-	-	0.33	0.09%
- Industrii agro-zootehnice		20.00	6.49%	28.04	6.39%
- Industrii si servicii de interes public		7.00	2.27%	13.82	3.08%
- Activitati de servicii		24.65	7.97%	30.76	6.87%
- Acti de comunicatie si transport, din care:		24.55	7.97%	30.75	6.87%
- Feroviar		-	-	-	-
- Spatiu verde, sport, agrement, protectie		0.98	0.32%	20.90	4.65%
- Zone verzi de protectie		-	-	2.48	0.55%
- Zone verzi de recreere		-	-	18.42	4.10%
Construcii tehnico-ediliciale		1.87	0.57%	-	-
Gospodaria comunală-civilă		4.35	1.41%	3.71	0.83%
Destinatie speciala		3.80	1.23%	15.08	3.37%
Alte		1.00	0.32%	0.19	0.04%
TOTAL		308.07	100.00%	443.26	100.00%

OBIECTIVE DE PATRIMONIUL			
Ind.	Obiectiv		Datare sec. XIX
P2	IMI C3-8-m-B-7686 ⁸ Căminul Teofil Conașc Pătrășchiv-Horath	Juza de Sus Juza de Sus	
P3	IMI C3-8-m-B-7087 ⁹ RAN 06206 02	"Starștie"	
P5	IMI C3-8-m-B-7087-01 ¹⁰	Tumul	"Starștie"
P6	IMI C3-8-m-B-7087-01 ¹¹	Așezare	Perioada de epoca bronzului, Cultura Crișanilor Neolitic
P6		Site arheologic punctul cimitii Biserici ortodoxe	"Cimitia" cimitia bisericii ortodoxe
P7	IMI C3-8-m-B-7086 ¹² RAN 58265 01	Site arheologic Budălia M. Site arheologic Budălia Mare	Epoca romană
P8		Chor	"Bucălia" Neolitic Sec. III-II p. Chr.
P9	IMI + Lista monumentelor istorice - RAN + Repertoriul Arheologic	Juza de Sus	

⁸ Obiective Datare în Lista Monumentelor istorice (IMI 2015) se află sub îndrumarea Legii 422/2001

UNITĂȚI TERITORIALE DE REFERINȚĂ ÎN EXTRAVILAN	
TDA	Terenuri cu destinație agricolă
A	Terenuri aflate permanent sub ape
A_S	Terenuri cu rol de cultur ecologic și turistic aferent Someșului
P	Terenuri cu destinație forestieră
TDS	Terenuri cu destinație specială
UNITĂȚI TERITORIALE DE REFERINȚĂ ÎN INTRAVILAN	
Lr	Zonă de locuințe rurale
S_Lr	Zonă de sistematizare pentru locuințe rurale
Ls	Zonă de locuințe sociale
Lsc	Zonă de locuințe semicolective
S_Lsc	Zonă de sistematizare pentru locuințe semicolective
Lc	Zonă locuințe colective
S_Lc	Zonă de sistematizare pentru locuințe colective
IS	Zonă de instituii publice și servicii
S_IS	Zonă de sistematizare pentru instituii publice și servicii
Lr	Zonă mixtă de locuințe rurale și servicii
Ta	Zonă de turism și agrement
S_Ta	Zonă de sistematizare pentru turism și agrement
S_LTa	Zonă de sistematizare pentru locuințe și turism / agrement
Et	Zonă de activități economice cu caracter terțiar
Uld	Zonă de unități industriale și depozitare
UN	Zonă de unități industriale mici cu caracter nepoluant
S_UN	Zonă de sistematizare pentru unități industriale mici cu caracter nepoluant
Ua	Zonă de unități agricole
Vg	Zonă verde cu rol de protecție și coridor ecologic
Ua	Zonă verde de agrement și sport
Gc	Zonă gospodărie comunală
E	Zonă aferentă construcțiilor tehnico-edilitare
TDS	Zonă cu destinație specială
TDS-Mapn	Zonă cu destinație specială- MAPN
Ccr	Zonă căi de comunicație rutieră și amenajări aferente



LEGENDĂ		ZONE PROTEJATE ȘI ZONE DE PROTECȚIE	
	Limita UAȚ Jucu		Imobil cu valoare de patrimoniu
	Limita intravilan propriu		Obiectiv cu valoare de patrimoniu înscris în Lista monumentelor istorice din 2015
	Limita zonei centrale		Sit arheologic
	Limita unităților teritoriale de referință (UTR)		Zona de protecție față de obiective cu valoare de patrimoniu
DRUMURI			Zonă de protecție sanitară (surse de apă, înmagazinări, stații de epurare sau uzate, ferme agrozoologice, etc.)
	Drum județean		Zonă de protecție față de construcții și culturile tehnice (stăți electrice, linii de înaltă tensiune, rețele de gaze, etc.)
	Drum comunal		Căminul verde al Someșului (drum de halaj, piste de biciclete, traseu pietonal, dîpi și zone de relaxare)
	Traseu propriu Someș Express	ZONE CU RISURI NATURALE	
	Traseu propriu piste de biciclete în lungul Someșului		Zonă cu risc de inundabilitate 1%
	Străzi, ulițe, drumuri de exploatare		Zonă cu risc de inundabilitate 5%
	Străzi propuse spre modernizare/propuse		Zona cu potențial de alunecare moderat
Lucrări Tehnico-Edilitare			Zona de izvoare sărate - se impun soluții speciale de fundare
	Linie electrică aeriană LEA 400kV		
	Linie electrică aeriană LEA 110kV		

OBJECTIVE – EXISTENTE	
Ind.	Objective
1	Primarie
2	Politie
3	Scoala ajutoare
4	Scoala generata
5	Biserica ortodoxa
6	Cimitir
7	Mic comert si alimentatie publica
8	Casa de rugaciuni
9	Posta
10	Microscriptie sanitar-veterinara
11	Circa
12	Complex comercial
13	Magazie
14	Statie de transformare
15	Zona speciala
16	Teren de sport
17	Parc
18	Casa memoriala "George Baritru"
19	Monument eroilor
20	Farmă de păsări – 150 000 de capete
21	Farmă zootehnică
22	Farmă bovine – 400 de capete
OBJECTIVE – PROPUSE	
A	Pod peste Someș
B	Piața de picnicetarie în Lungul Someșului
C	AlinaC
D	Not rutier: Someș Express
E	Zona de agrement sărături

