


6.2

Reglementări urbanistice - UTR, sat Vișea

REACTUALIZARE
P.U.G
COMUNA JUCU
JUDEȚUL CLUJ

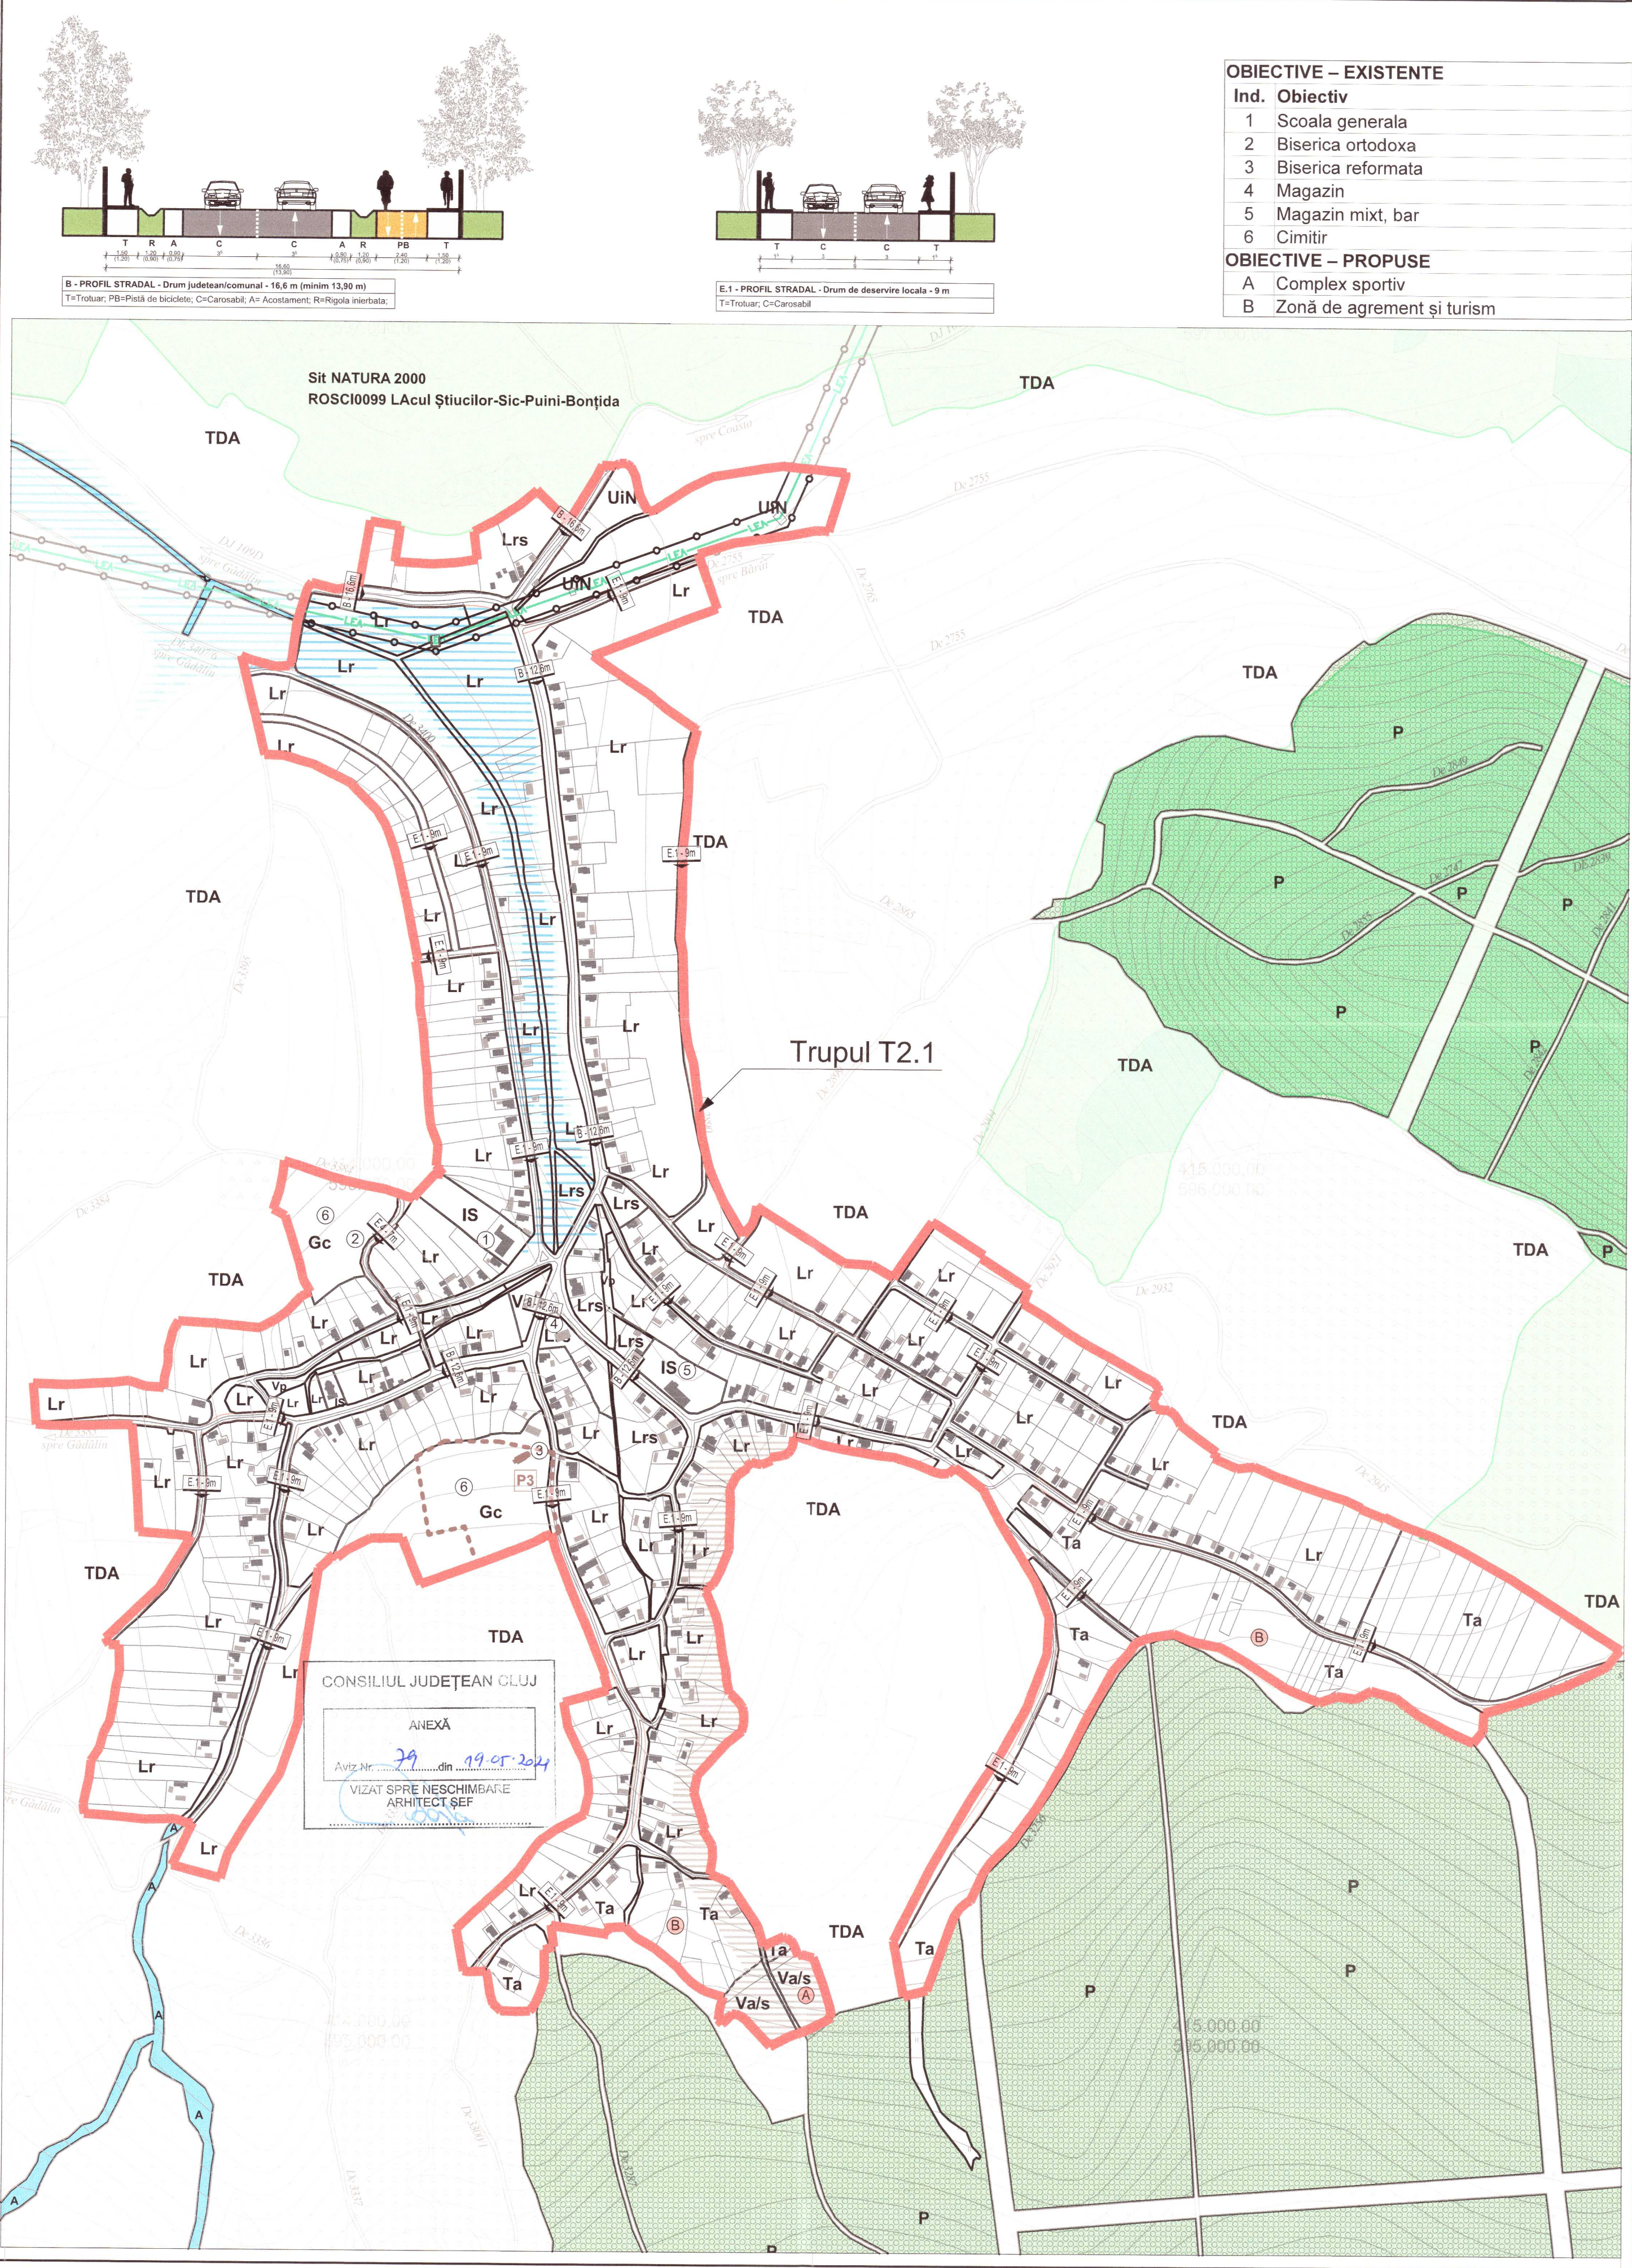

LEGENDĂ

LIMITE

Limita UAT Jucu

Limita intravilan propus

Limita zonei centrale

Limita unităților teritoriale de referință (UTR)

ZONE CU RISCURI NATURALE

Zona cu potențial de alunecare moderat

Zona cu risc de inundabilitate 1%

Zona cu risc de inundabilitate 5%

ZONE PROTEJATE ȘI ZONE DE PROTECȚIE

Sit de importanță comunitară Natura 2000

Zonă de protecție sanitară (surse de apă, înmagazinări, stații de epurare ape uzate, ferme agrozootehnice, etc.)

Zonă de protecție față de construcții și culoare tehnice (stații electrice, linii de înaltă tensiune, rețele de gaze, etc.)

Imobil cu valoare de patrimoniu

LUCRĂRI TEHNICO-EDILITARE

Linie electrică aeriană LEA 20kV

DRUMURI

Drum județean

Străzi, ulițe, drumuri de exploatare

BILANTUL TERITORIAL AL SUPRAFETELOR CUPRINSE ÎN INTRAVILAN				
Zona funcționala	Situația existentă		Situația propusă	
	Suprafața		Suprafața	
	HA	%	HA	%
Locuințe și funcțiuni complementare	68,30	75,05%	62,54	60,92%
• Locuire rurala	-	-	62,54	60,92%
• Locuire colectivă	-	-	0,00	0,00%
• Locuire semicolectivă	-	-	0,00	0,00%
Zona mixtă – locuire și servicii	-	-	3,66	3,57%
Unități industriale și depozitare	3,70	4,07%	3,00	2,92%
• Parc industrial	-	-	0,00	0,00%
• Producție industrială cu caracter nepoluant	-	-	3,00	2,92%
Unități agro-zootehnice	0,00	0,00%	0,00	0,00%
Instituiții și servicii de interes public	1,30	1,43%	1,12	1,09%
Cai de comunicație și transport, din care:	7,00	7,69%	12,21	11,89%
• rutier	7,00	7,69%	12,21	11,89%
• feroviar	-	-	0,00	0,00%
Spatii verzi, sport, agrement, protecție	6,80	7,47%	14,35	13,98%
• Zone verzi cu acces public nelimitat	-	-	1,08	1,05%
• Zone verzi de protecție	-	-	0,14	0,14%
• Zona de agrement public/privat	-	-	13,13	12,79%
Construcții tehnico-edilitare	-	-	0,01	0,01%
Gospodărie comunală-cimitire	2,70	2,97%	4,16	4,05%
Destinație specială	0,00	-	0,00	0,00%
Ape	1,20	1,32%	1,61	1,57%
TOTAL	91,00	100,00%	102,66	100,00%

OBIECTIVE DE PATRIMONIU			
Ind.	Obiectiv		Date
P3	Biserica reformată din Vișea	Vișea	sec. XIX

UNITĂȚI TERITORIALE DE REFERINȚĂ ÎN EXTRAVILAN	
TDA	Terenuri cu destinație agricolă
A	Terenuri aflate permanent sub ape
A S	Zonă cu rol de culoar ecologic și turistic aferent Someșului
P	Terenuri cu destinație forestieră
TDS	Terenuri cu destinație specială
UNITĂȚI TERITORIALE DE REFERINȚĂ ÎN INTRAVILAN	
Lr	Zonă de locuințe rurale
IS	Zonă de instituții publice și servicii
Lrs	Zonă mixtă de locuințe rurale și servicii
Ta	Zonă de turism și agrement
UiN	Zonă de unități industriale mici cu caracter nepoluant
Vp	Zonă verde cu rol de protecție și coridor ecologic
Va/s	Zonă verde de agrement și sport
Gc	Zonă gospodărire comunală
E	Zonă aferentă construcțiilor tehnico-edilitare
Ccr	Zonă cai de comunicație rutieră și amenajări aferente

SEF PROIECT arh. Horatiu Racasan			PROIECTANT S.C. RAUM S.R.L. Str. Octavian Goga, nr. 41, Cluj-Napoca, jud. Cluj, Romania email: raumoffice@gmail.com arh. Horatiu Racasan tel. 0723-624272 membru O.A.R. / membru R.U.R.	BENEFICIARI COMUNA JUCU reprezentata prin Pojar Valentin Dorel	NR. PROIECT 42
PROIECTAT arh. Crina Petca					
DESENAT arh. Crina Petca					
VERIFICAT arh. Horatiu Racasan					
DENUMIREA PLANSEI NR. PLANSA 6.2		REACTUALIZARE PLAN URBANISTIC GENERAL (PUG) COMUNA JUCU, JUD. CLUJ			
Reglementări urbanistice - UTR, sat Vișea					
FAZA PUG	SCARA 1:5000	DATA 2020			