6.4

Reglementări urbanistice - UTR, sat Jucu de Mijloc

REACTUALIZARE
P.U.G
COMUNA JUCU
JUDEȚUL CLUJ

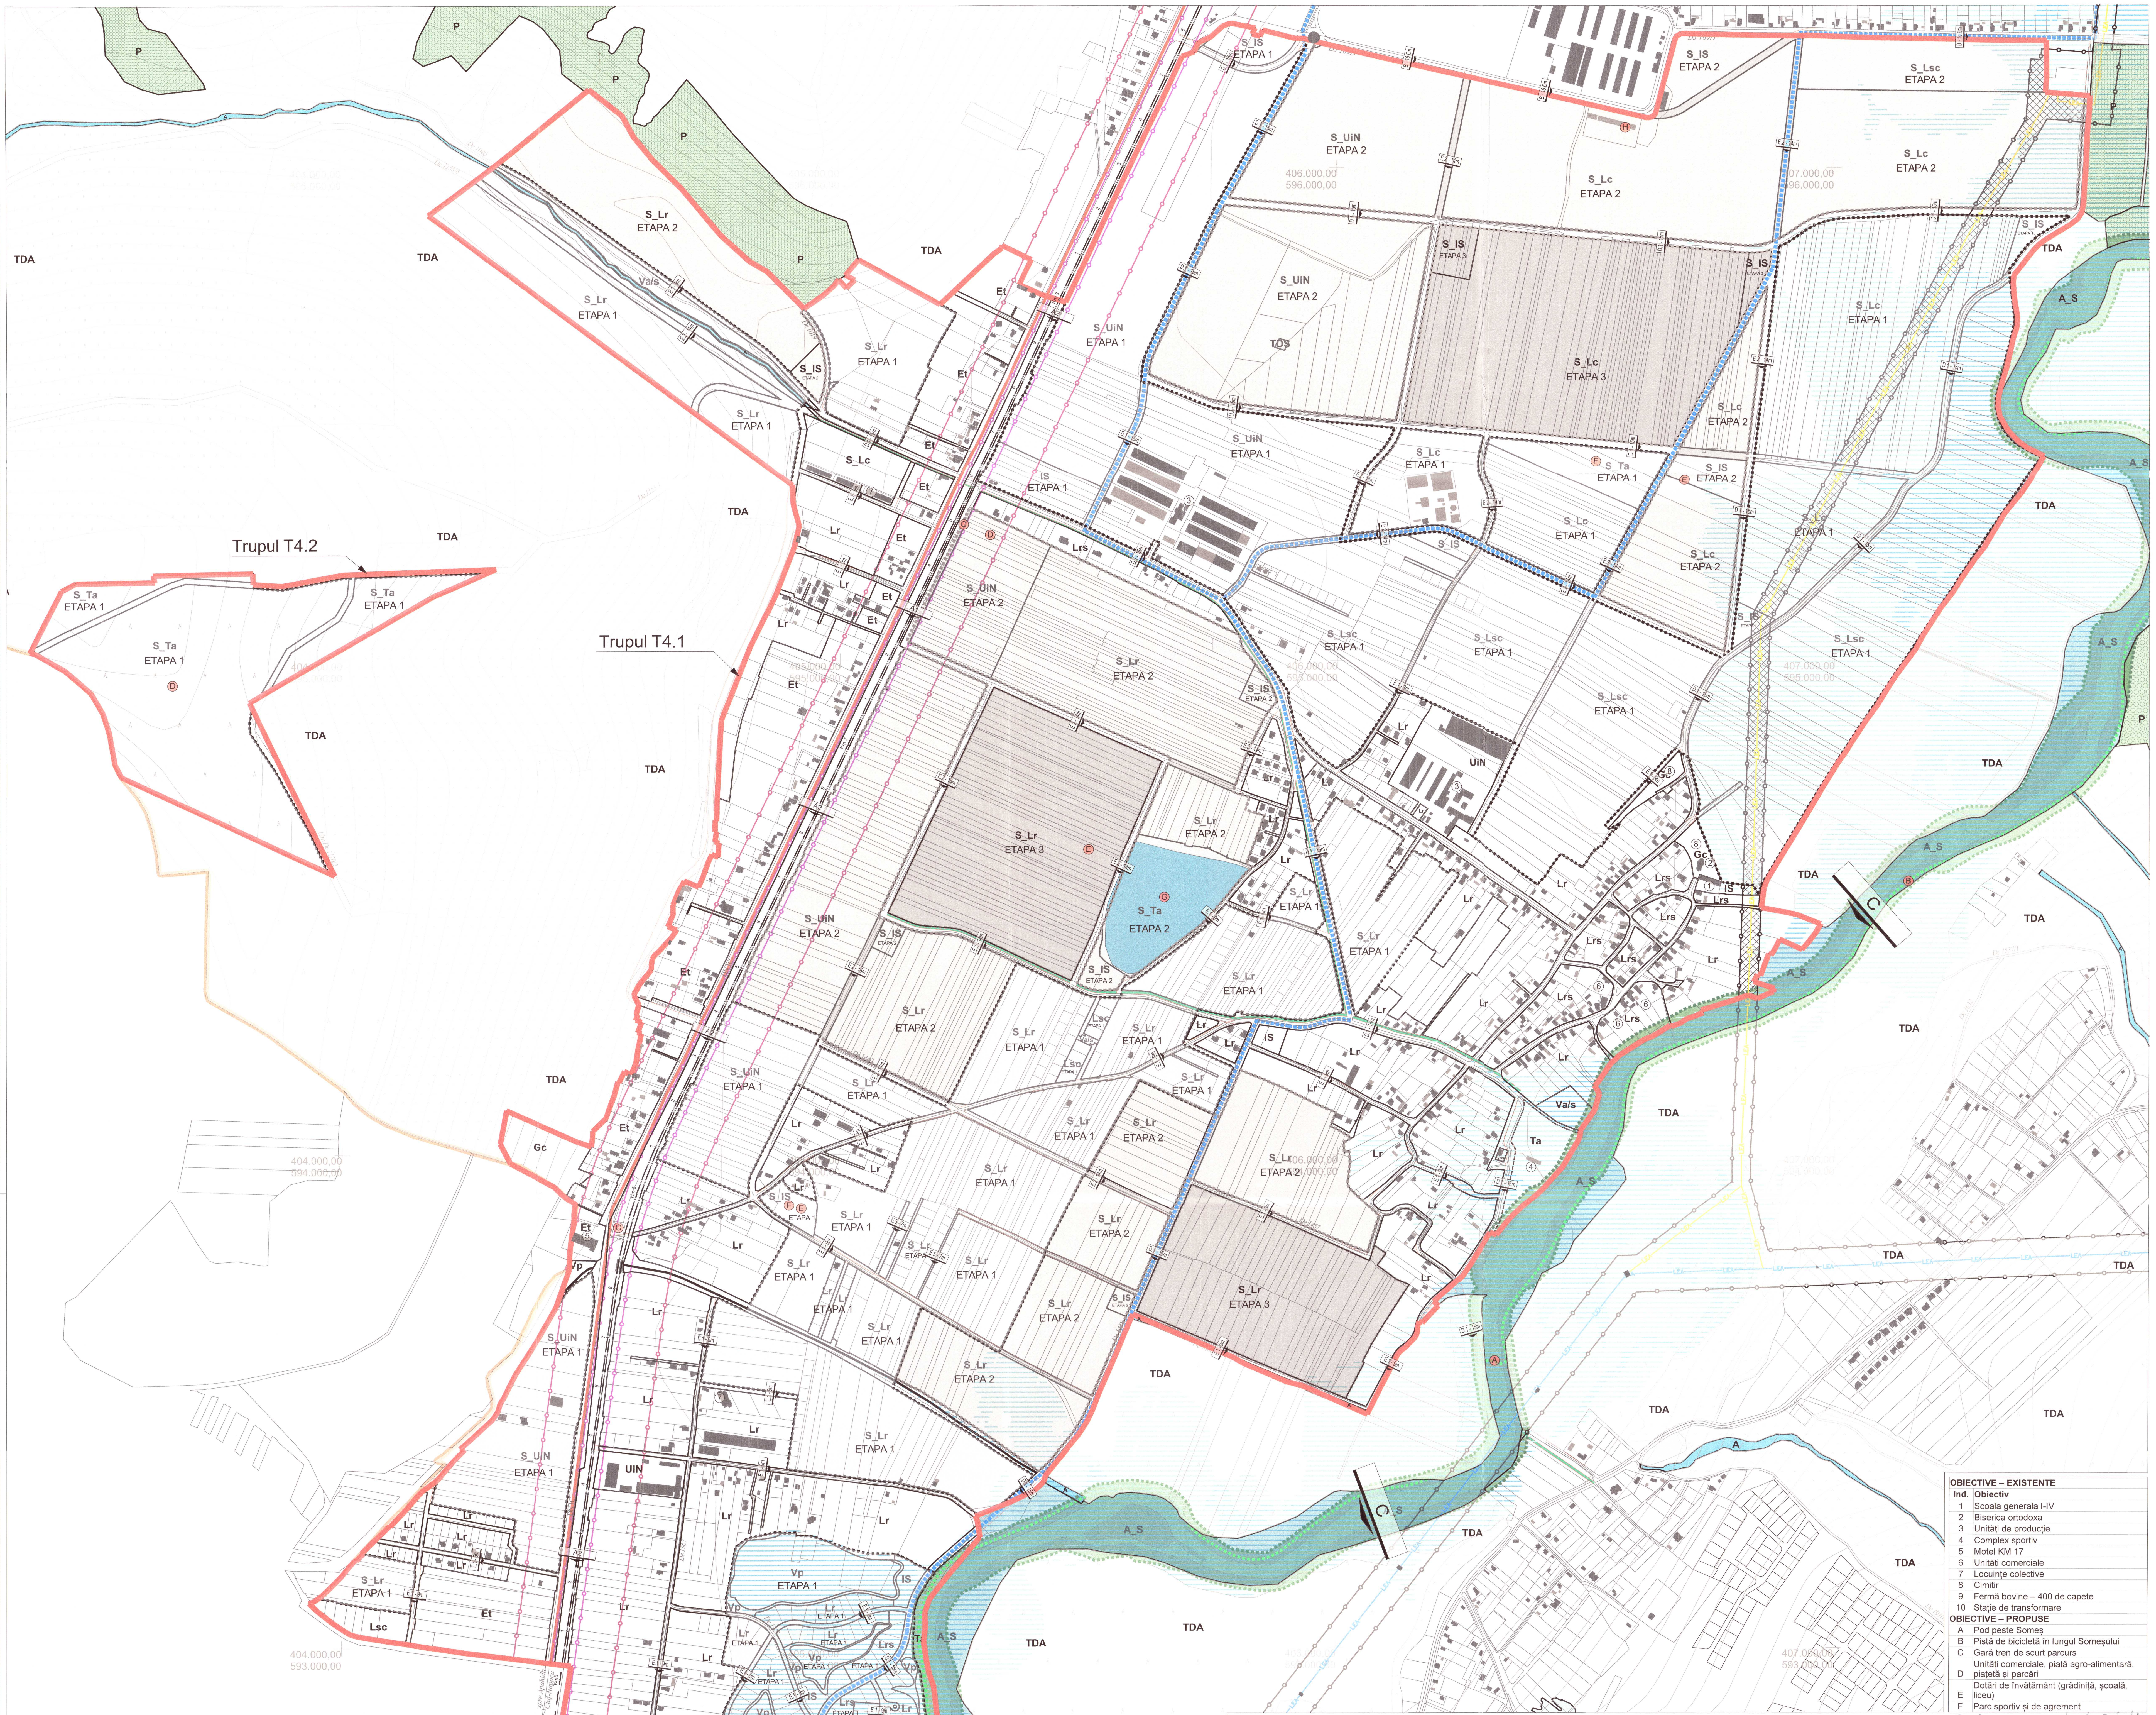

BILANTUL TERITORIAL AL SUPRAFETELOR CUPRINSE IN INTRAVILAN

Zona functionala	Situatia existenta Suprafata HA	Situatia existenta Suprafata %	Situatia propusa Suprafata HA	Situatia propusa Suprafata %
Locuinte si functiuni complementare	150.84	74.66%	438.93	61.33%
▪ *Locuire rurala*	-	-	*268.74*	*37.55%*
▪ *Locuire colectiva*	-	-	*104.13*	*14.55%*
▪ *Locuire semicolectiva*	-	-	*66.06*	*9.23%*
Zona mixta – locuire si servicii	-	-	11.69	1.63%
Activități economice cu caracter terțiar	-	-	28.73	4.01%
Unitati industriale si depozitare	22.70	11.24%	103.52	14.46%
▪ *Parc industrial*	-	-	*0.00*	*0.00%*
▪ *Productie industriala cu caracter nepoluant*	-	-	*103.52*	*14.46%*
Unitati agro-zootehnice	3.00	1.48%	0.00	0.00%
Institutii si servicii de interes public	1.60	0.79%	12.15	1.70%
Cai de comunicatie si transport, din care:	12.00	5.94%	67.90	9.49%
▪ *rutier*	12.00	*5.94%*	*60.41*	*8.44%*
▪ *feroviar*	-	-	*7.49*	*1.05%*
Spatii verzi, sport, agrement, protectie	5.80	2.87%	43.28	6.05%
▪ *Zone verzi cu acces public nelimitat*	-	-	*5.89*	*0.82%*
▪ *Zone verzi de protectie*	-	-	*2.93*	*0.41%*
▪ *Zona de agrement public/privat*	-	-	*34.46*	*4.82%*
Constructii tehnico-edilitare	-	-	0.00	0.00%
Gospodarie comunala-cimitire	3.50	1.73%	2.67	0.37%
Destinatie speciala	0.00	-	0.04	0.01%
Ape	2.60	1.29%	6.77	0.95%
TOTAL	***202.04***	***100.00%***	***715.68***	***100.00%***

UNITĂȚI TERITORIALE DE REFERINȚĂ ÎN EXTRAVILAN	
TDA	Terenuri cu destinație agricolă
A	Terenuri aflate permanent sub ape
A_S	Zonă cu rol de culoar ecologic și turistic aferent Someșului
P	Terenuri cu destinație forestieră
TDS	Terenuri cu destinație specială
UNITĂȚI TERITORIALE DE REFERINȚĂ ÎN INTRAVILAN	
Lr	Zonă de locuințe rurale
S_Lr	Zona de sistematizare pentru locuințe rurale
Ls	Zonă de locuințe sociale
Lsc	Zonă de locuințe semicolective
S_Lsc	Zonă de sistematizare pentru locuințe semicolective
Lc	Zonă locuințe colective
S_Lc	Zonă de sistematizare pentru Locuințe colective
IS	Zonă de instituții publice și servicii
S_IS	Zonă de sistematizare pentru instituții publice și servicii
Lrs	Zonă mixtă de locuințe rurale și servicii
Ta	Zonă de turism și agrement
S_Ta	Zonă de sistematizare pentru turism și agrement
S_LTa	Zonă de sistematizare pentru locuințe și turism / agrement
Et	Zonă de activități economice cu caracter terțiar
Ui/d	Zonă de unități industriale și depozitare
UiN	Zonă de unități industriale mici cu caracter nepoluant
S_UiN	Zonă de sistematizare pentru unități industriale mici cu caracter nepoluant
Ua	Zonă de unități agricole
Vp	Zonă verde cu rol de protecție și coridor ecologic
Va/s	Zonă verde de agrement și sport
Gc	Zonă gospodărire comunală
E	Zonă aferentă construcțiilor tehnico-edilitare
TDS	Zonă cu destinație specială
TDS-Mapn	Zonă cu destinație specială- MAPN
Ccr	Zonă căi de comunicație rutieră și amenajări aferente
Ccf	Zonă căi de comunicație feroviară și amenajări aferente

LEGENDĂ

LIMITE

╱	Limita UAT Jucu
╱	Limita intravilan propus
⋰	Limita zonei centrale
╱	Limita unităților teritoriale de referință (UTR)

DRUMURI

╱	Drum național
╱	Drum județean
⋰	Traseu propus Someș Expres
⋰	Traseu propus pistă de biciclete în lungul Someșului
╱	Străzi, uliţe, drumuri de exploatare
╱	Străzi propuse spre modernizare/propuse
⋰	Traseu propus : Transportul in comun- Autobuz

ZONE CU RISCURI NATURALE

▤	Zona cu risc de inundabilitate 1%
▤	Zona cu risc de inundabilitate 5%
▤	Zona cu potenţial de alunecare moderat

ZONE PROTEJATE ŞI ZONE DE PROTECŢIE

🟩	Sit de importanță comunitară Natura 2000
╱	Zonă de protecţie sanitară (surse de apă, înmagazinări, staţii de epurare ape uzate, ferme agrozootehnice, etc.)
╱	Zonă de protecţie faţă de construcţii şi culoare tehnice (staţii electrice, linii de înaltă tensiune, reţele de gaze, etc.)
╱	Zonă de protecţie faţă de infrastructura feroviară (100 metri din axul caii ferate)
╱	Zona de siguranță față de infrastructura feroviară (20 metri din axul caii ferate)
▨	Culoarul verde al Someșului (drum de halaj, pistă de biciclete, traseu pietonal, dig și zone de relaxare)

LUCRĂRI TEHNICO-EDILITARE

╱	Linie electrică aeriană LEA 400kV
╱	Linie electrică aeriană LEA 110kV

ETAPIZARE

⬚	ETAPA 1
⬚	ETAPA 2
▩	ETAPA 3

OBIECTIVE – EXISTENTE	
Ind.	**Obiectiv**
1	Scoala generala I-IV
2	Biserica ortodoxa
3	Unități de producție
4	Complex sportiv
5	Motel KM 17
6	Unități comerciale
7	Locuințe colective
8	Cimitir
9	Fermă bovine – 400 de capete
10	Stație de transformare
OBIECTIVE – PROPUSE	
A	Pod peste Someș
B	Pistă de bicicletă în lungul Someșului
C	Gară tren de scurt parcurs
D	Unități comerciale, piață agro-alimentară, piațetă și parcări
E	Dotări de învățământ (grădiniță, școală, liceu)
F	Parc sportiv și de agrement

G = Loc de agrement, alimentație publică
H = Locuințe sociale

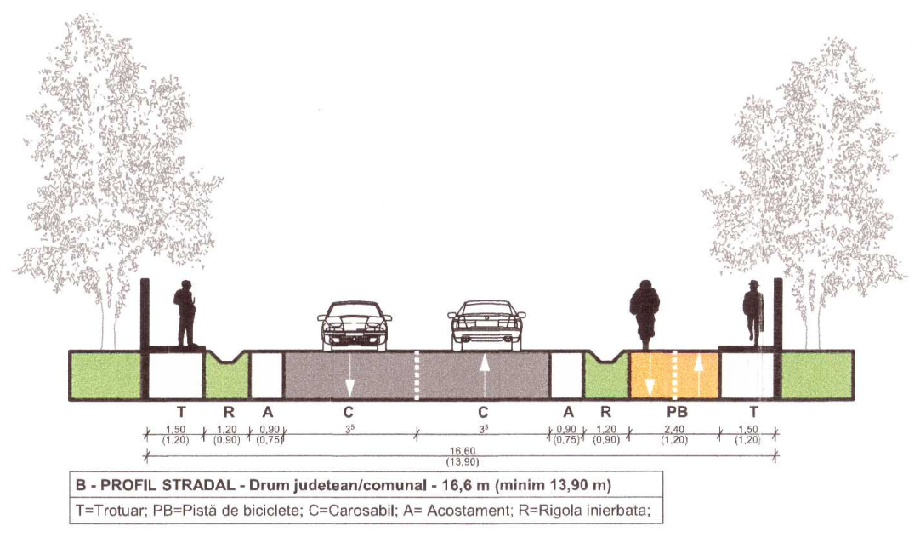

B - PROFIL STRADAL - Drum judetean/comunal - 16,6 m (minim 13,90 m)
T=Trotuar; PB=Pistă de biciclete; C=Carosabil; A= Acostament; R=Rigola inierbata;

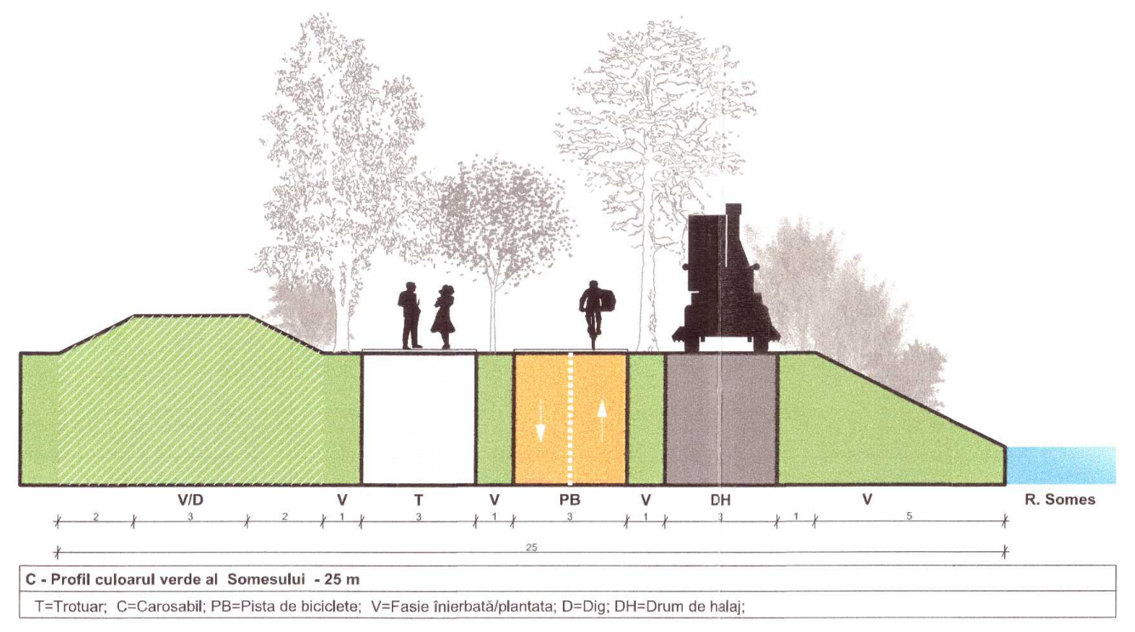

C - Profil culoarul verde al Somesului - 25 m
T=Trotuar; C=Carosabil; PB=Pista de biciclete; V=Fasie înierbată/plantata; D=Dig; DH=Drum de halaj;

CONSILIUL JUDEȚEAN CLUJ
ANEXĂ
Aviz Nr. 79 din 19.05.2014
VIZAT SPRE NESCHIMBARE
ARHITECT ȘEF

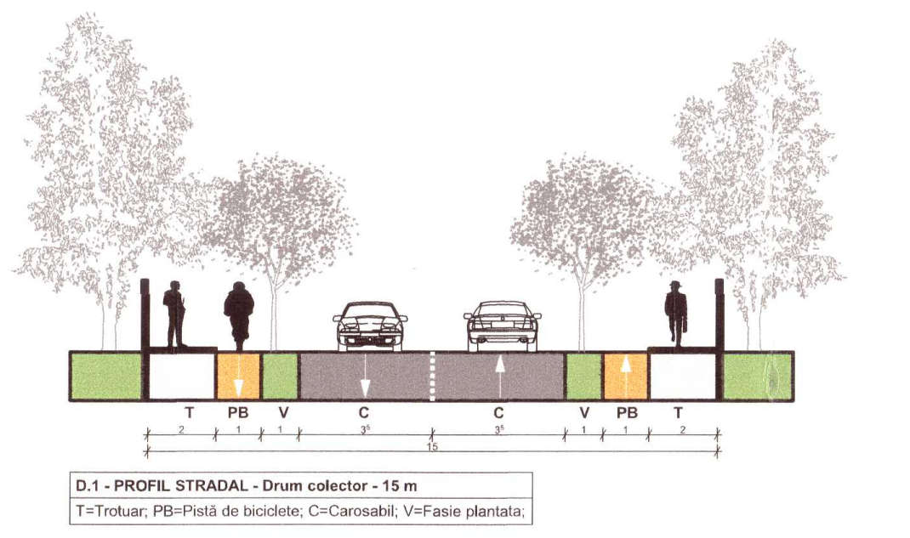

D.1 - PROFIL STRADAL - Drum colector - 15 m
T=Trotuar; PB=Pistă de biciclete; C=Carosabil; V=Fasie plantata;

Horațiu Șerban I. RĂCĂȘAN arhitect

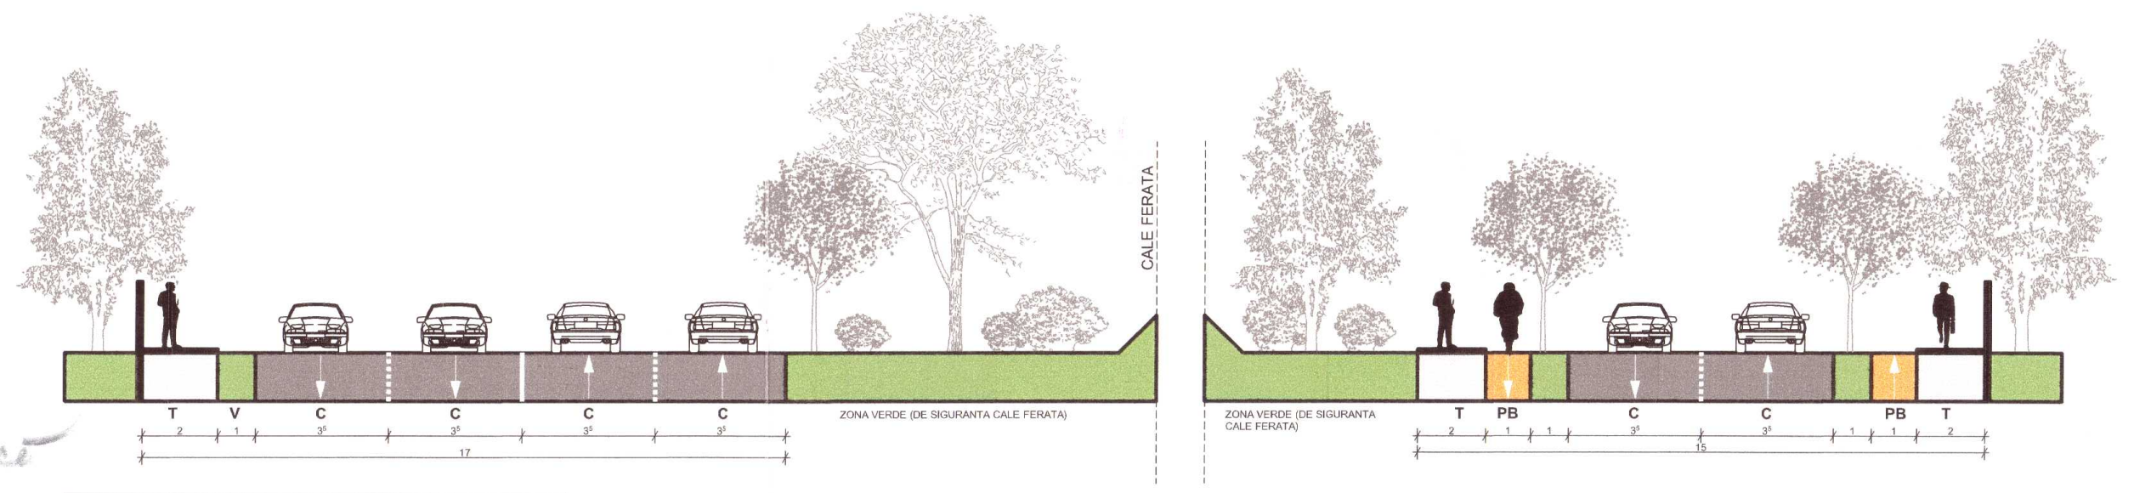
T
V
C
C
C
C
ZONA VERDE (DE SIGURANTA CALE FERATA)
CALE FERATA
ZONA VERDE (DE SIGURANTA CALE FERATA)
T
PB
C
C
PB
T
2
1
3⁵
3⁵
3⁵
3⁵
17
2
1
1
3⁵
3⁵
1
1
2
15

A.1 - PROFIL STRADAL - DN 1C, Calea ferata si Drum colector
T=Trotuar; PB=Pistă de biciclete; C=Carosabil; V=Fasie plantata

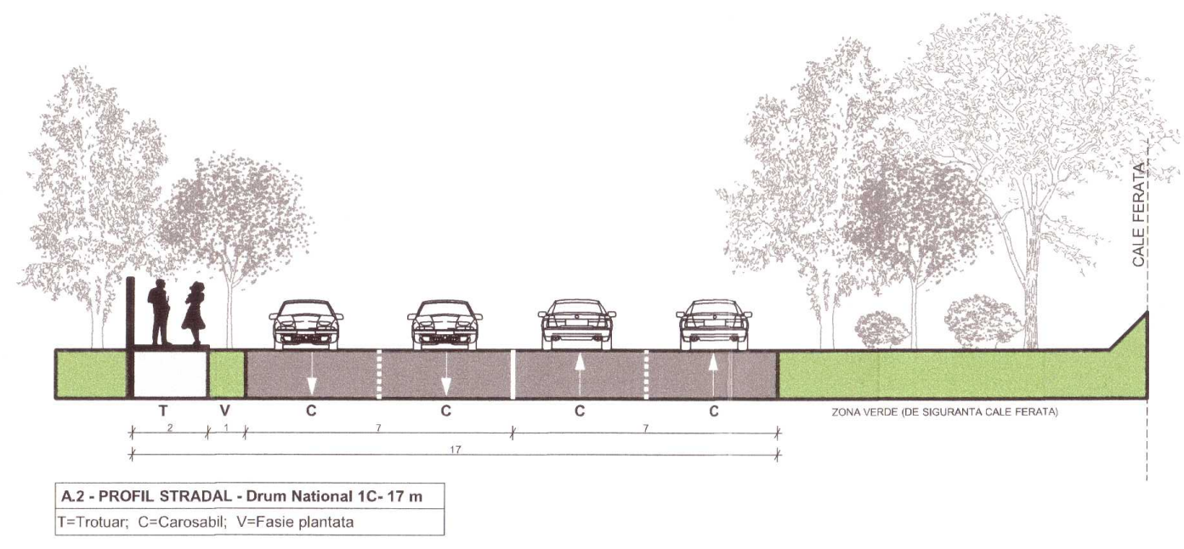

A.2 - PROFIL STRADAL - Drum National 1C- 17 m
T=Trotuar; C=Carosabil; V=Fasie plantata

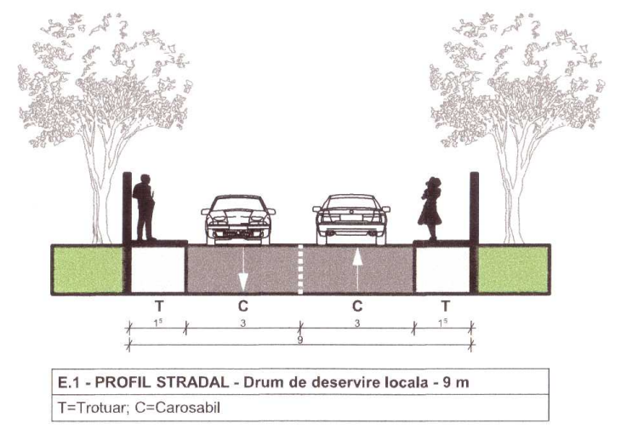

E.1 - PROFIL STRADAL - Drum de deservire locala - 9 m
T=Trotuar; C=Carosabil

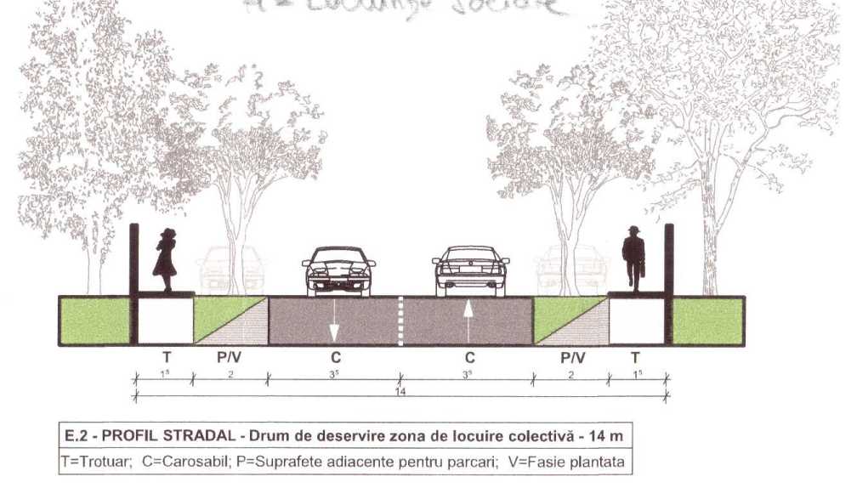

E.2 - PROFIL STRADAL - Drum de deservire zona de locuire colectivă - 14 m
T=Trotuar; C=Carosabil; P=Suprafete adiacente pentru parcari; V=Fasie plantata

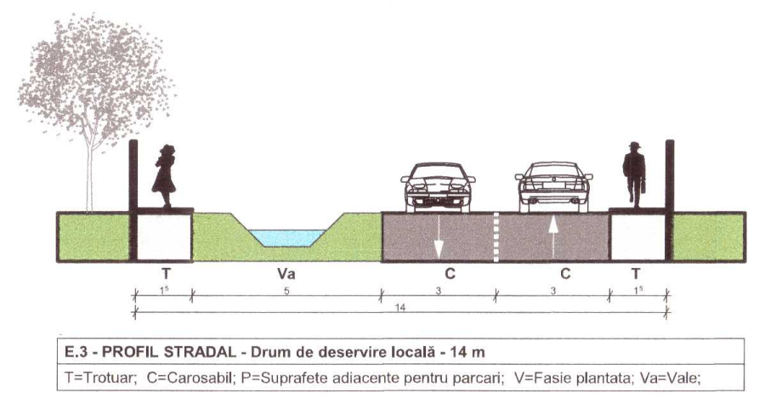

E.3 - PROFIL STRADAL - Drum de deservire locală - 14 m
T=Trotuar; C=Carosabil; P=Suprafete adiacente pentru parcari; V=Fasie plantata; Va=Vale;

Acest document este proprietatea firmei SC RAUM SRL si nu poate fi folosit, transmis sau reprodus, total sau partial, fara autorizarea expresa si scrisa. Utilizarea sa trebuie sa fie conforma celei pentru care a fost elaborat. Documentul este valabil numai cu semnaturile si stampila proiectantilor in original.

SEF PROIECT	arh. Horatiu Racasan		**PROIECTANT** **S.C. RAUM S.R.L.** Str. Octavian Goga, nr. 41, Cluj-Napoca, jud. Cluj, Romania **email: raumoffice@gmail.com** **arh. Horaţiu Răcăşan tel. 0723-624272** **membru O.A.R. / membru R.U.R.**	
PROIECTAT	arh. Crina Petca			
DESENAT	arh. Crina Petca			
VERIFICAT	arh. Horatiu Racasan			
DENUMIREA PLANSEI		NR. PLANSA	BENEFICIARI	NR. PROIECT
Reglementări urbanistice - UTR, sat Jucu de Mijloc		**6.4**	**COMUNA JUCU** **reprezentata prin Pojar Valentin Dorel**	**42**
FAZA	SCARA	DATA	DENUMIREA LUCRARII:	
PUG	**1:5000**	**2020**	**REACTUALIZARE PLAN URBANISTIC GENERAL (PUG) COMUNA JUCU, JUD. CLUJ**	