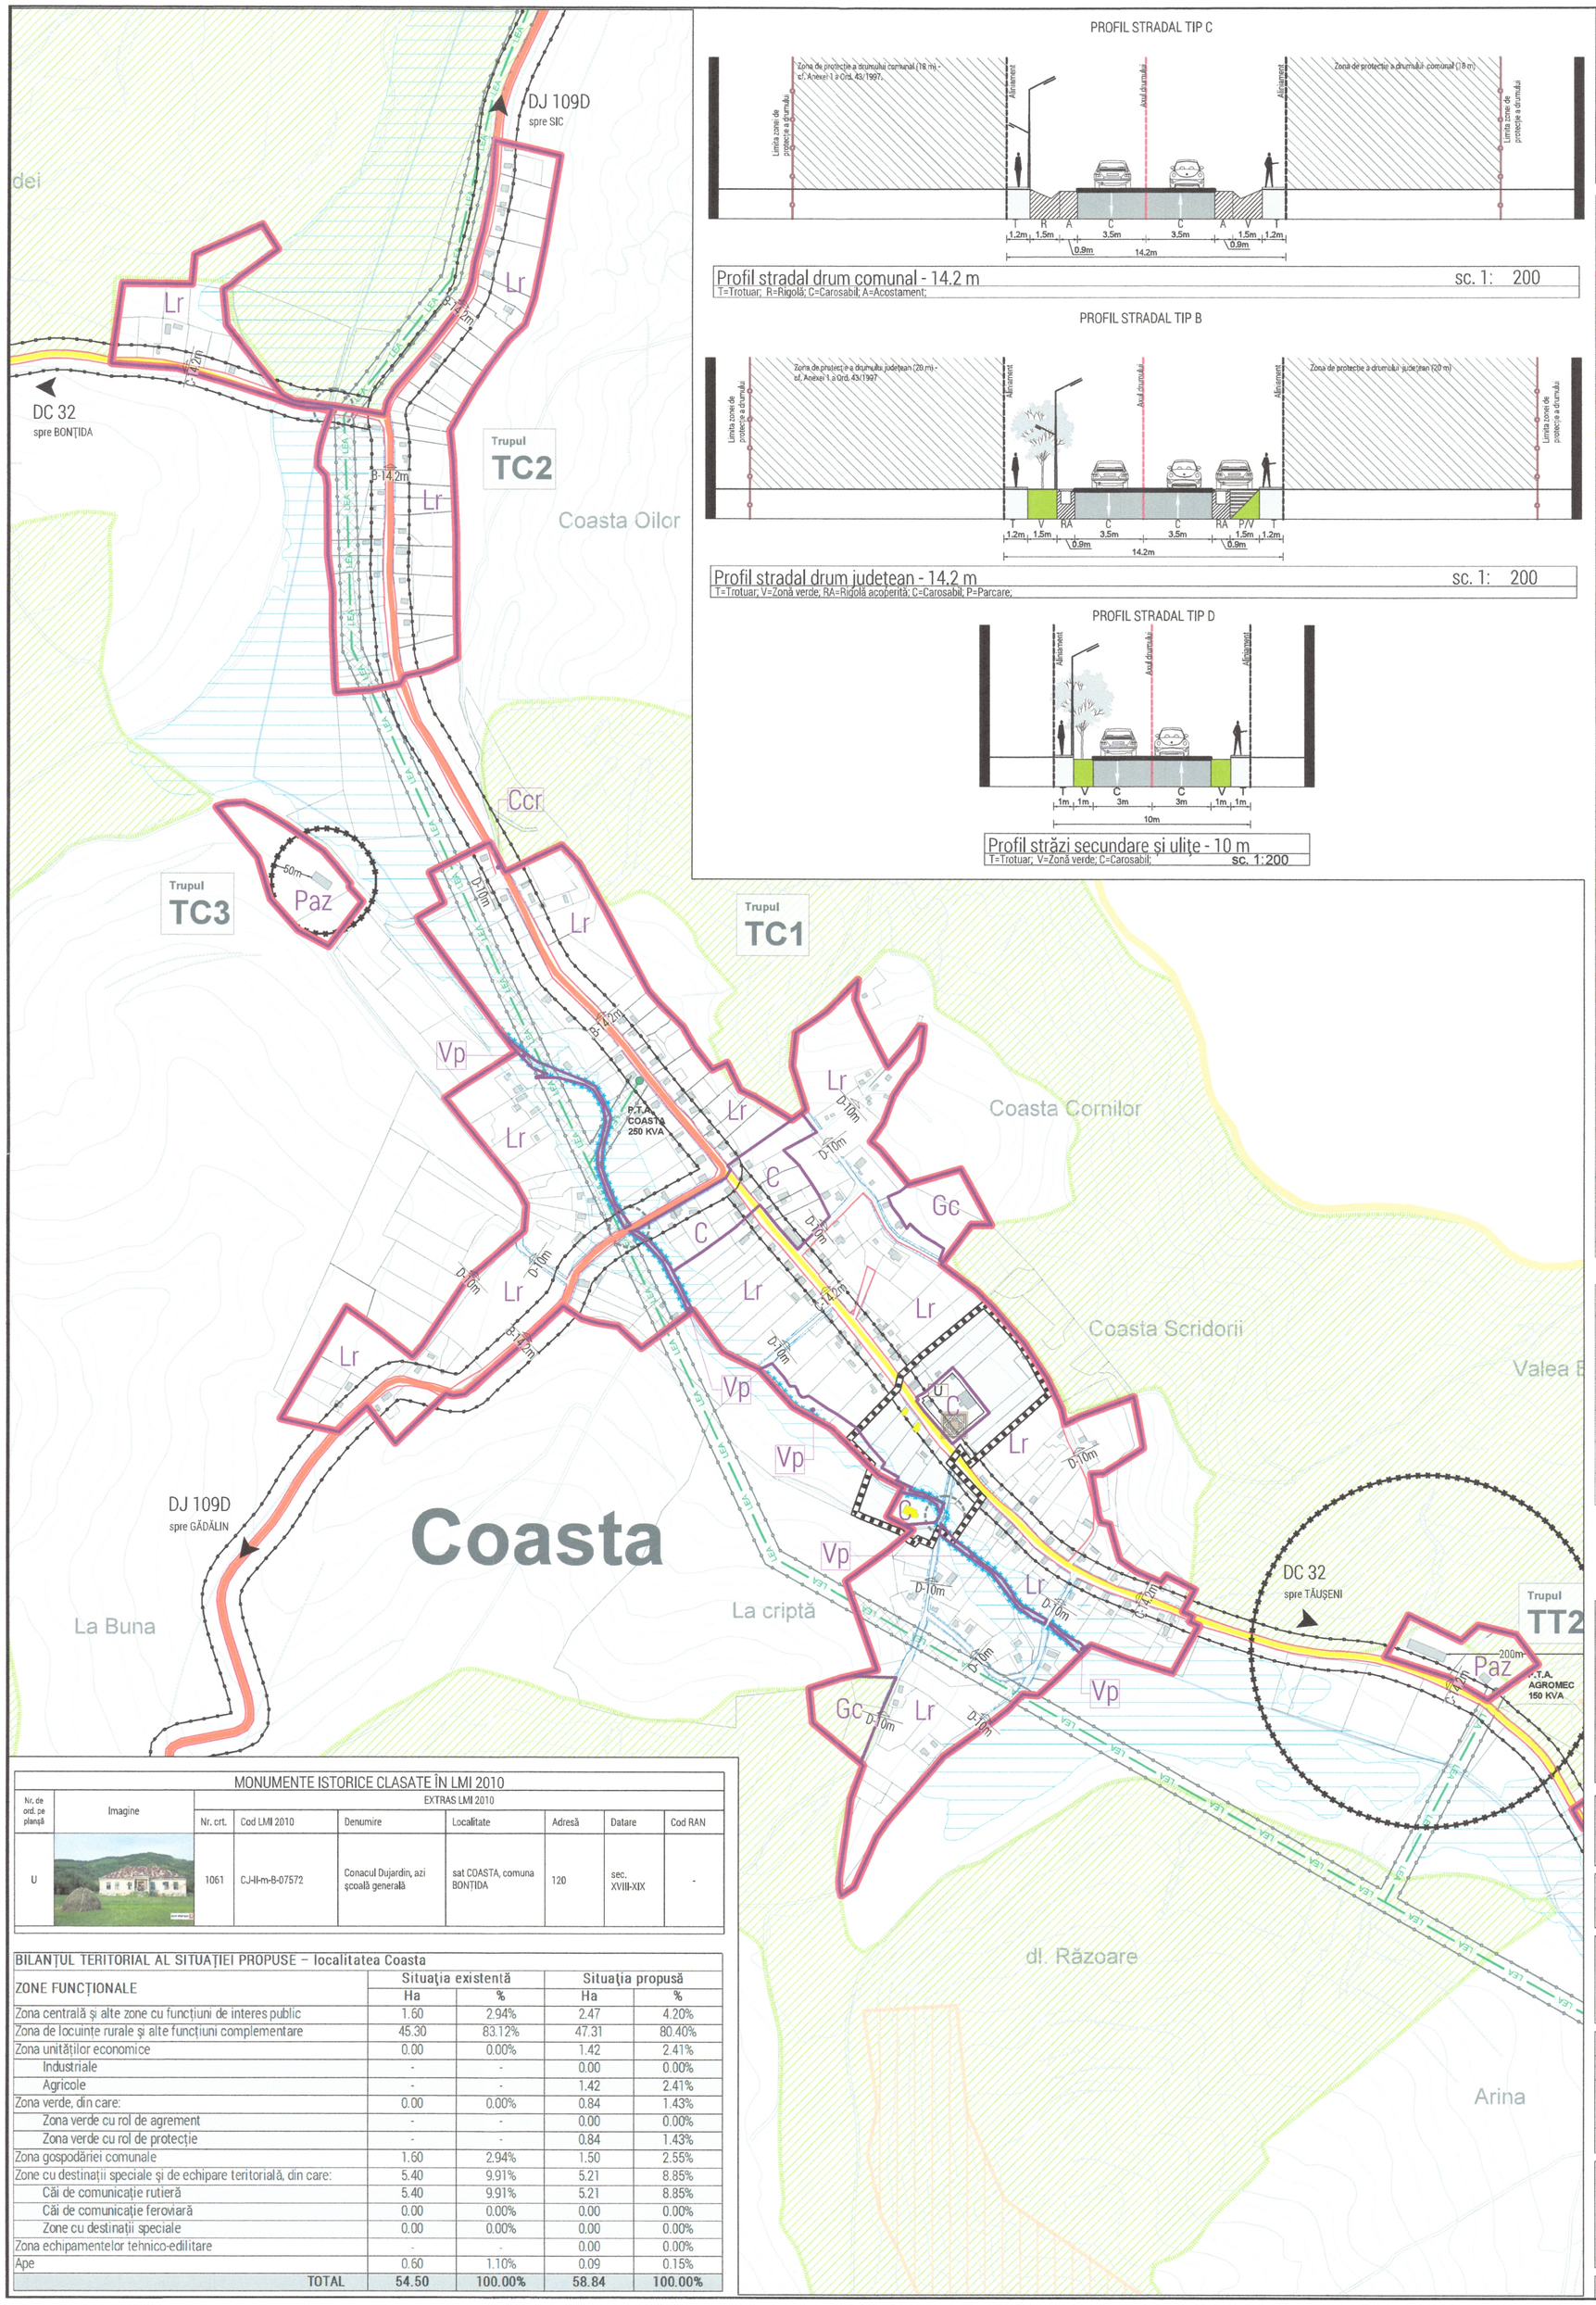


PROFIL STRADAL TIP C

Profil stradal drum comunal - 14.2 m sc. 1: 200

T=Trotuar; R=Rigolă; C=Carosabil; A=Acostament;

PROFIL STRADAL TIP B

Profil stradal drum județean - 14.2 m sc. 1: 200

T=Trotuar; V=Zonă verde; RA=Rigolă acoperită; C=Carosabil; P=Parcare;

PROFIL STRADAL TIP D

Profil străzi secundare și ulițe - 10 m sc. 1:200

T=Trotuar; V=Zonă verde; C=Carosabil;

MONUMENTE ISTORICE CLASATE ÎN LMI 2010								
Nr. de ord. pe planșă	Imagine	EXTRAS LMI 2010						
		Nr. crt.	Cod LMI 2010	Denumire	Localitate	Adresă	Datare	Cod RAN
U		1061	CJ-II-m-B-07572	Conacul Dujardin, azi școală generală	sat COASTA, comuna BONȚIDA	120	sec. XVIII-XIX	-

BILANȚUL TERITORIAL AL SITUAȚIEI PROPUSE – localitatea Coasta				
ZONE FUNCȚIONALE	Situația existentă		Situația propusă	
	Ha	%	Ha	%
Zona centrală și alte zone cu funcțiuni de interes public	1.60	2.94%	2.47	4.20%
Zona de locuințe rurale și alte funcțiuni complementare	45.30	83.12%	47.31	80.40%
Zona unităților economice	0.00	0.00%	1.42	2.41%
Industriale	-	-	0.00	0.00%
Agricole	-	-	1.42	2.41%
Zona verde, din care:	0.00	0.00%	0.84	1.43%
Zona verde cu rol de agrement	-	-	0.00	0.00%
Zona verde cu rol de protecție	-	-	0.84	1.43%
Zona gospodăriei comunale	1.60	2.94%	1.50	2.55%
Zone cu destinații speciale și de echipare teritorială, din care:	5.40	9.91%	5.21	8.85%
Căi de comunicație rutieră	5.40	9.91%	5.21	8.85%
Căi de comunicație feroviară	0.00	0.00%	0.00	0.00%
Zone cu destinații speciale	0.00	0.00%	0.00	0.00%
Zona echipamentelor tehnico-edilitare	-	-	0.00	0.00%
Ape	0.60	1.10%	0.09	0.15%
TOTAL	54.50	100.00%	58.84	100.00%

N

P.U.G.

COMUNA **BONȚIDA**
SAT **COASTA**

LEGENDĂ

LIMITE
- Limită intravilan propus
- Limită UAT Bonțida
- Limită unități teritoriale de referință (UTR)

CĂI DE COMUNICAȚIE
- Drum județean DJ 109D
- Drum comunal DC 32
- Străzi, uliță și alte drumuri neclasificate
- Drumuri propuse spre modernizare
- Poduri auto propuse spre reabilitare

REGLEMENTĂRI
- Monument istoric clasat în LMI 2010
- Zona de protecție monument istoric (ZPMI)
- Clădiri cu valoare locală
- Zona de protecție sanitară *cf. Ord. 119/2014 pentru aprobarea Normelor de igienă și sănătate publică privind mediul de viață al populației*
- Interdicție de construire locuințe până la obținerea avizului Direcției de Sănătate Publică
- Zona de protecție a cursurilor de apă
- Zona de protecție drum județean (20m), comunal (18m), cf. Anexei nr. 1 a Ord. 43/1997 privind regimul drumurilor - se va solita avizul administratorului drumului
- Interdicție temporară de construire - în zonele de protecție tehnologică a LEA, magistrala de apă, gaz și zona de siguranță a infrastructurii feroviare

ZONE NATURALE PROTEJATE
- Zonă naturală protejată Natura 2000 ROSCI0295 Dealurile Clujului Est și ROSCI0099 Lacul Știucilor-Sic-Puini-Bonțida - obligativitate obținere aviz Custode

ZONE CE NECESITĂ MĂSURI DE PROTECȚIE ÎMPOTRIVA RISCURILOR NATURALE
- Zonă afectată de risc la inundații - obligativitate obținere aviz A.N. Apele Române - A.B. Someș-Tisa
- Zona cu risc mediu de alunecări de teren - K(m)=0,11-0.30 -

Pentru zonele cu potențial risc de alunecări de teren se va respecta NP-074-2014.
Pentru zonele cu risc mediu de alunecări de teren se vor întocmi studii de stabilitate.

CIRCULAȚIA TERENURILOR
- Terenuri ce se intenționează a fi trecute în domeniul public

ECHIPARE EDILITARĂ

ALIMENTARE CU ENERGIE ELECTRICĂ
- LEA — Linie electrică aeriană 20kV
- Post de transformare
- Limită culoar tehnic de protecție linie electrică aeriană (75 m-LEA 400kV, 24 m-LEA 20kV)

LEGENDĂ

UNITĂȚI TERITORIALE DE REFERINȚĂ

C	Zona centrală și alte zone cu funcțiuni de interes public
Lr	Zona de locuințe rurale și alte funcțiuni complementare
Paz	Zona unități economice agro-zootehnice
Gc	Zona gospodăriei comunale
Vp	Zona verde cu rol de protecție a apelor și cu rol de coridor ecologic

CONSILIUL JUDEȚEAN CLUJ
ANEXĂ
Avizul Nr. 135 din 13.08.2019
VIZAT SPRE NESCHIMBARE
ARHITECT ȘEF

Denumire proiect:
REACTUALIZARE PLAN URBANISTIC GENERAL (P.U.G.) AL COMUNEI BONȚIDA, JUDEȚUL CLUJ

Beneficiar: COMUNA BONȚIDA, JUDEȚUL CLUJ
Contract nr.: 14 / 2013, 101 / 2018

Proiectant: S.C. DARH PROIECTARE ARHITECTURA SI DESIGN S.R.L.
Cluj-Napoca, Str. General Traian Moșoiu, nr. 48/5-6
J12 / 2956 / 1993
Director: arh. T. Raiciu

	Nume:	Semnătura:
Șef proiect:	arh. Amalia Gyemant	
Proiectat:	arh. Amalia Gyemant	
	arh. Patricia Miron	
Desenat:	arh. Patricia Miron	

Denumire planșă:
REGLEMENTĂRI - UNITĂȚI TERITORIALE DE REFERINȚĂ
sat COASTA, comuna BONȚIDA, județul Cluj

Nr. planșă: **5.3**

Scara: 1:5 000
Data: 2018