

MONUMENTE ISTORICE CLASATE ÎN LMI 2010							
Nr. de ord. pe planșă	Imagine	Nr. crt.	Cod LMI 2010	Denumire	Localitate	Adresă	Cod RAN
V		612	C-H-s-A-07204*	Așezare	sat TĂUȘENI, comuna BONȚIDA	"Dealul Piculești"	56256.01


LEGENDĂ

UNITĂȚI TERITORIALE DE REFERINȚĂ

C	Zona centrală și alte zone cu funcțiuni de interes public
Lr	Zona de locuințe rurale și alte funcțiuni complementare
Paz	Zona unități economice agro-zootehnice
Gc	Zona gospodăriei comunale
Va	Zona verde cu rol de agrement
Vp	Zona verde cu rol de protecție a apelor și cu rol de coridor ecologic

BILANȚUL TERITORIAL AL SITUAȚIEI PROPUSE – localitatea Tăușeni

ZONE FUNCȚIONALE	Situația existentă		Situația propusă	
	Ha	%	Ha	%
Zona centrală și alte zone cu funcțiuni de interes public	1.00	2.15%	1.36	2.39%
Zona de locuințe rurale și alte funcțiuni complementare	39.10	83.91%	44.62	78.39%
Zona unităților economice	0.70	1.50%	1.10	1.93%
Industriale	-	-	0.00	0.00%
Agricole	-	-	1.10	1.93%
Zona verde, din care:	0.00	0.00%	4.33	7.61%
Zona verde cu rol de agrement	-	-	3.10	5.45%
Zona verde cu rol de protecție	-	-	1.23	2.16%
Zona gospodăriei comunale	0.50	1.07%	0.46	0.81%
Zone cu destinații speciale și de echipare teritorială, din care:	4.20	9.01%	4.90	8.61%
Căi de comunicație rutieră	4.20	9.01%	4.90	8.61%
Căi de comunicație feroviară	0.00	0.00%	0.00	0.00%
Zone cu destinații speciale	0.00	0.00%	0.00	0.00%
Zona echipamentelor tehnico-edilitare	-	-	0.00	0.00%
Ape	1.10	2.36%	0.15	0.26%
TOTAL	46.60	100.00%	56.92	100.00%

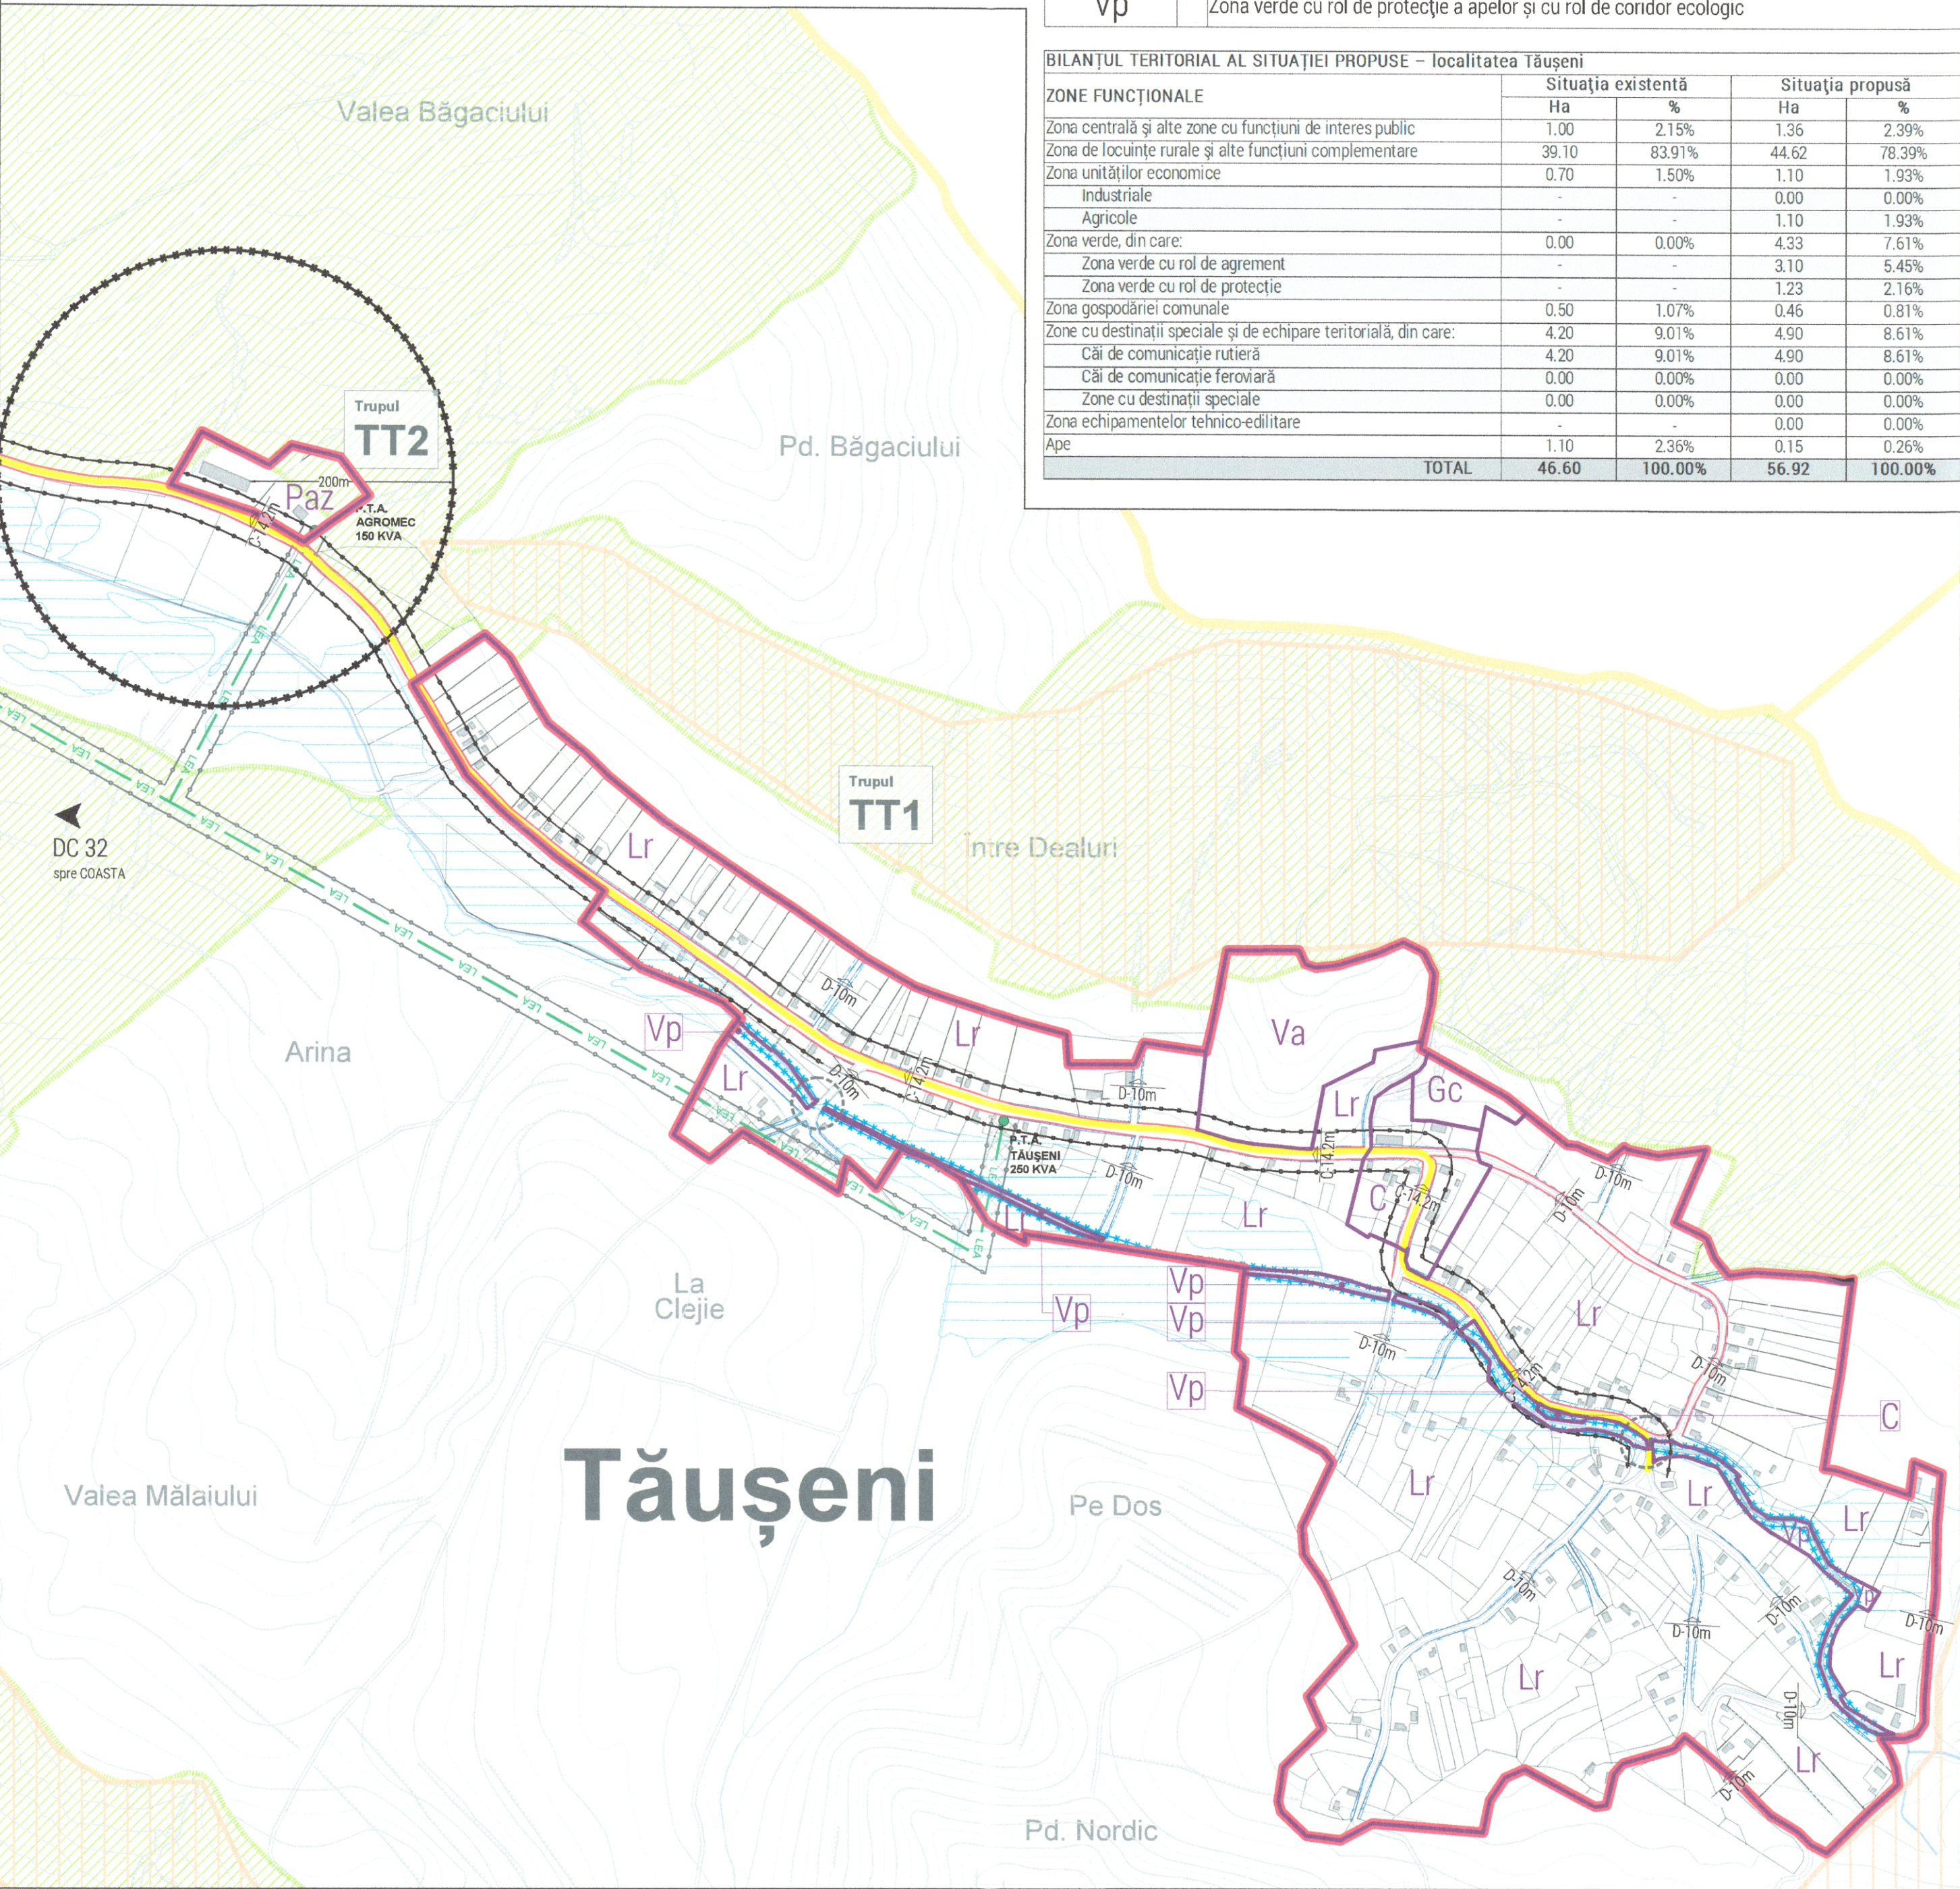

Tăușeni

Valea Mălaiului


Arina

La Clejje

Pe Dos

Pd. Nordic

PROFIL STRADAL TIP C

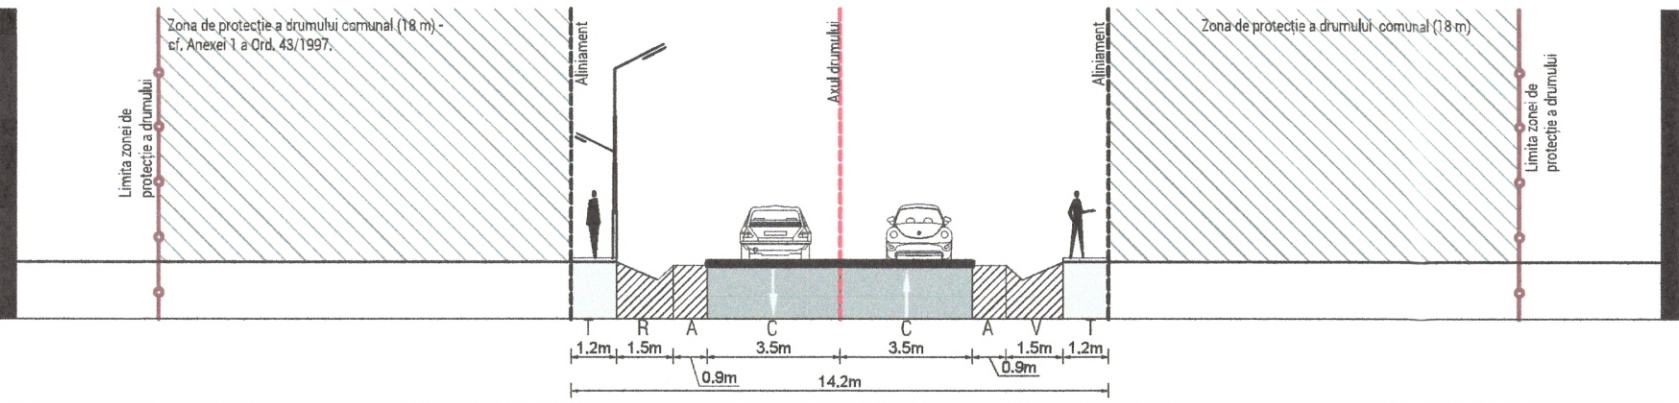


Profil stradal drum comunal - 14.2 m

T=Trotuar, R=Rigolă, C=Carosabil, A=Acostament;

sc. 1: 200

PROFIL STRADAL TIP D

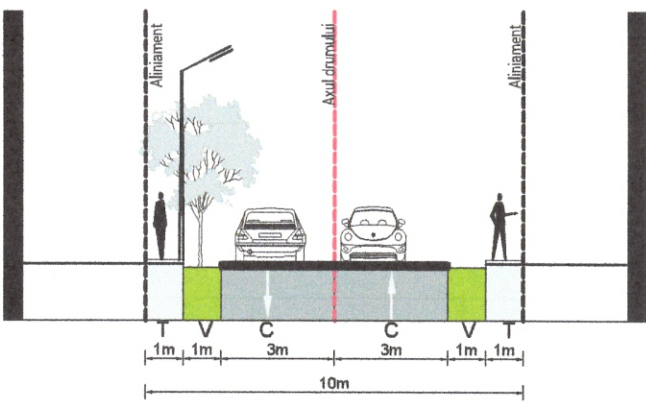

Profil străzi secundare și ulițe - 10 m

T=Trotuar, V=Zona verde, C=Carosabil;

sc. 1:200

P.U.G.

COMUNA **BONȚIDA**
SAT **TĂUȘENI**

LEGENDĂ

LIMITE

	Limită intravilan propus
	Limită UAT Bonțida
	Limită unități teritoriale de referință (UTR)

CĂI DE COMUNICAȚIE

	Drum județean DJ 109D
	Drum comunal DC 32
	Străzi, ulițe și alte drumuri neclasificate
	Drumuri propuse spre modernizare
	Poduri auto propuse spre reabilitare

REGLEMENTĂRI

	Monument istoric clasat în LMI 2010
	Zonă de protecție monument istoric
	Zona de protecție sanitară cf. Ord. 119/2014 pentru aprobarea Normelor de igienă și sănătate publică privind mediul de viață al populației
	Zona de protecție a cursurilor de apă
	Zona de protecție drum județean (20m), comunal (18m), cf. Anexei nr. 1 a Ord. 43/1997 privind regimul drumurilor - se va solita avizul administratorului drumului
	Interdicție temporară de construire - în zonele de protecție tehnologică a LEA, magistrala de apă, gaz și zona de siguranță a infrastructurii feroviare

ZONE NATURALE PROTEJATE

	Zonă naturală protejată Natura 2000 ROSCI0295 Dealurile Clujului Est și ROSCI0099 Lacul Știucilor-Sic-Puini-Bonțida - obligativitate obținere aviz Custode
--	--

ZONE CE NECESITĂ MĂSURI DE PROTECȚIE ÎMPOTRIVA RISCURILOR NATURALE

	Zonă afectată de risc la inundații - obligativitate obținere aviz A.N. Apelor Române - A.B. Someș-Tisa
	Zona cu risc mediu de alunecări de teren - K(m)=0,11-0.30 -

Pentru zonele cu potențial risc de alunecări de teren se va respecta NP-074-2014.

Pentru zonele cu risc mediu și mediu-mare de alunecări de teren se vor întocmi studii de stabilitate.

CIRCULAȚIA TERENURILOR

	Terenuri ce se intenționează a fi trecute în domeniul public
--	--

ECHIPARE EDILITARĂ

ALIMENTARE CU ENERGIE ELECTRICĂ

	LEA	Linie electrică aeriană 20kV
		Post de transformare
		Limită culoar tehnic de protecție linie electrică aeriană (75 m-LEA 400kV, 24 m-LEA 20kV)

CONSILIUL JUDEȚEAN CLUJ

ANEXĂ

Aviz Nr. 935 din 13.08.2019

VIZAT SPRE NESCIMBARE ARHITECT ȘEF

Denumire proiect:

REACTUALIZARE PLAN URBANISTIC GENERAL (P.U.G.) AL COMUNEI BONȚIDA, JUDEȚUL CLUJ

Beneficiar:	COMUNA BONȚIDA, JUDEȚUL CLUJ	Contract nr.: 14 / 2013, 101 / 2018
-------------	------------------------------	-------------------------------------

Proiectant:	S.C. DARH PROIECTARE ARHITECTURA SI DESIGN S.R.L. Cluj-Napoca, Str. General Traian Moșoiu, nr. 48/5-6 J12 / 2956 / 1993	Director: arh. T. Raiciu
-------------	---	--------------------------

Șef proiect:	Nume: arh. Amalia Gyemant	Semnătura:	
Proiectat:	arh. Amalia Gyemant		
Desenat:	arh. Patricia Miron		

DARH
PROIECTARE ARHITECTURA SI DESIGN

Denumire planșă:

REGLEMENTĂRI - UNITĂȚI TERITORIALE DE REFERINȚĂ sat TĂUȘENI, comuna BONȚIDA, județul Cluj	Nr. planșă: 5.4
--	-----------------

Scara: 1:5 000

Data: 2018