


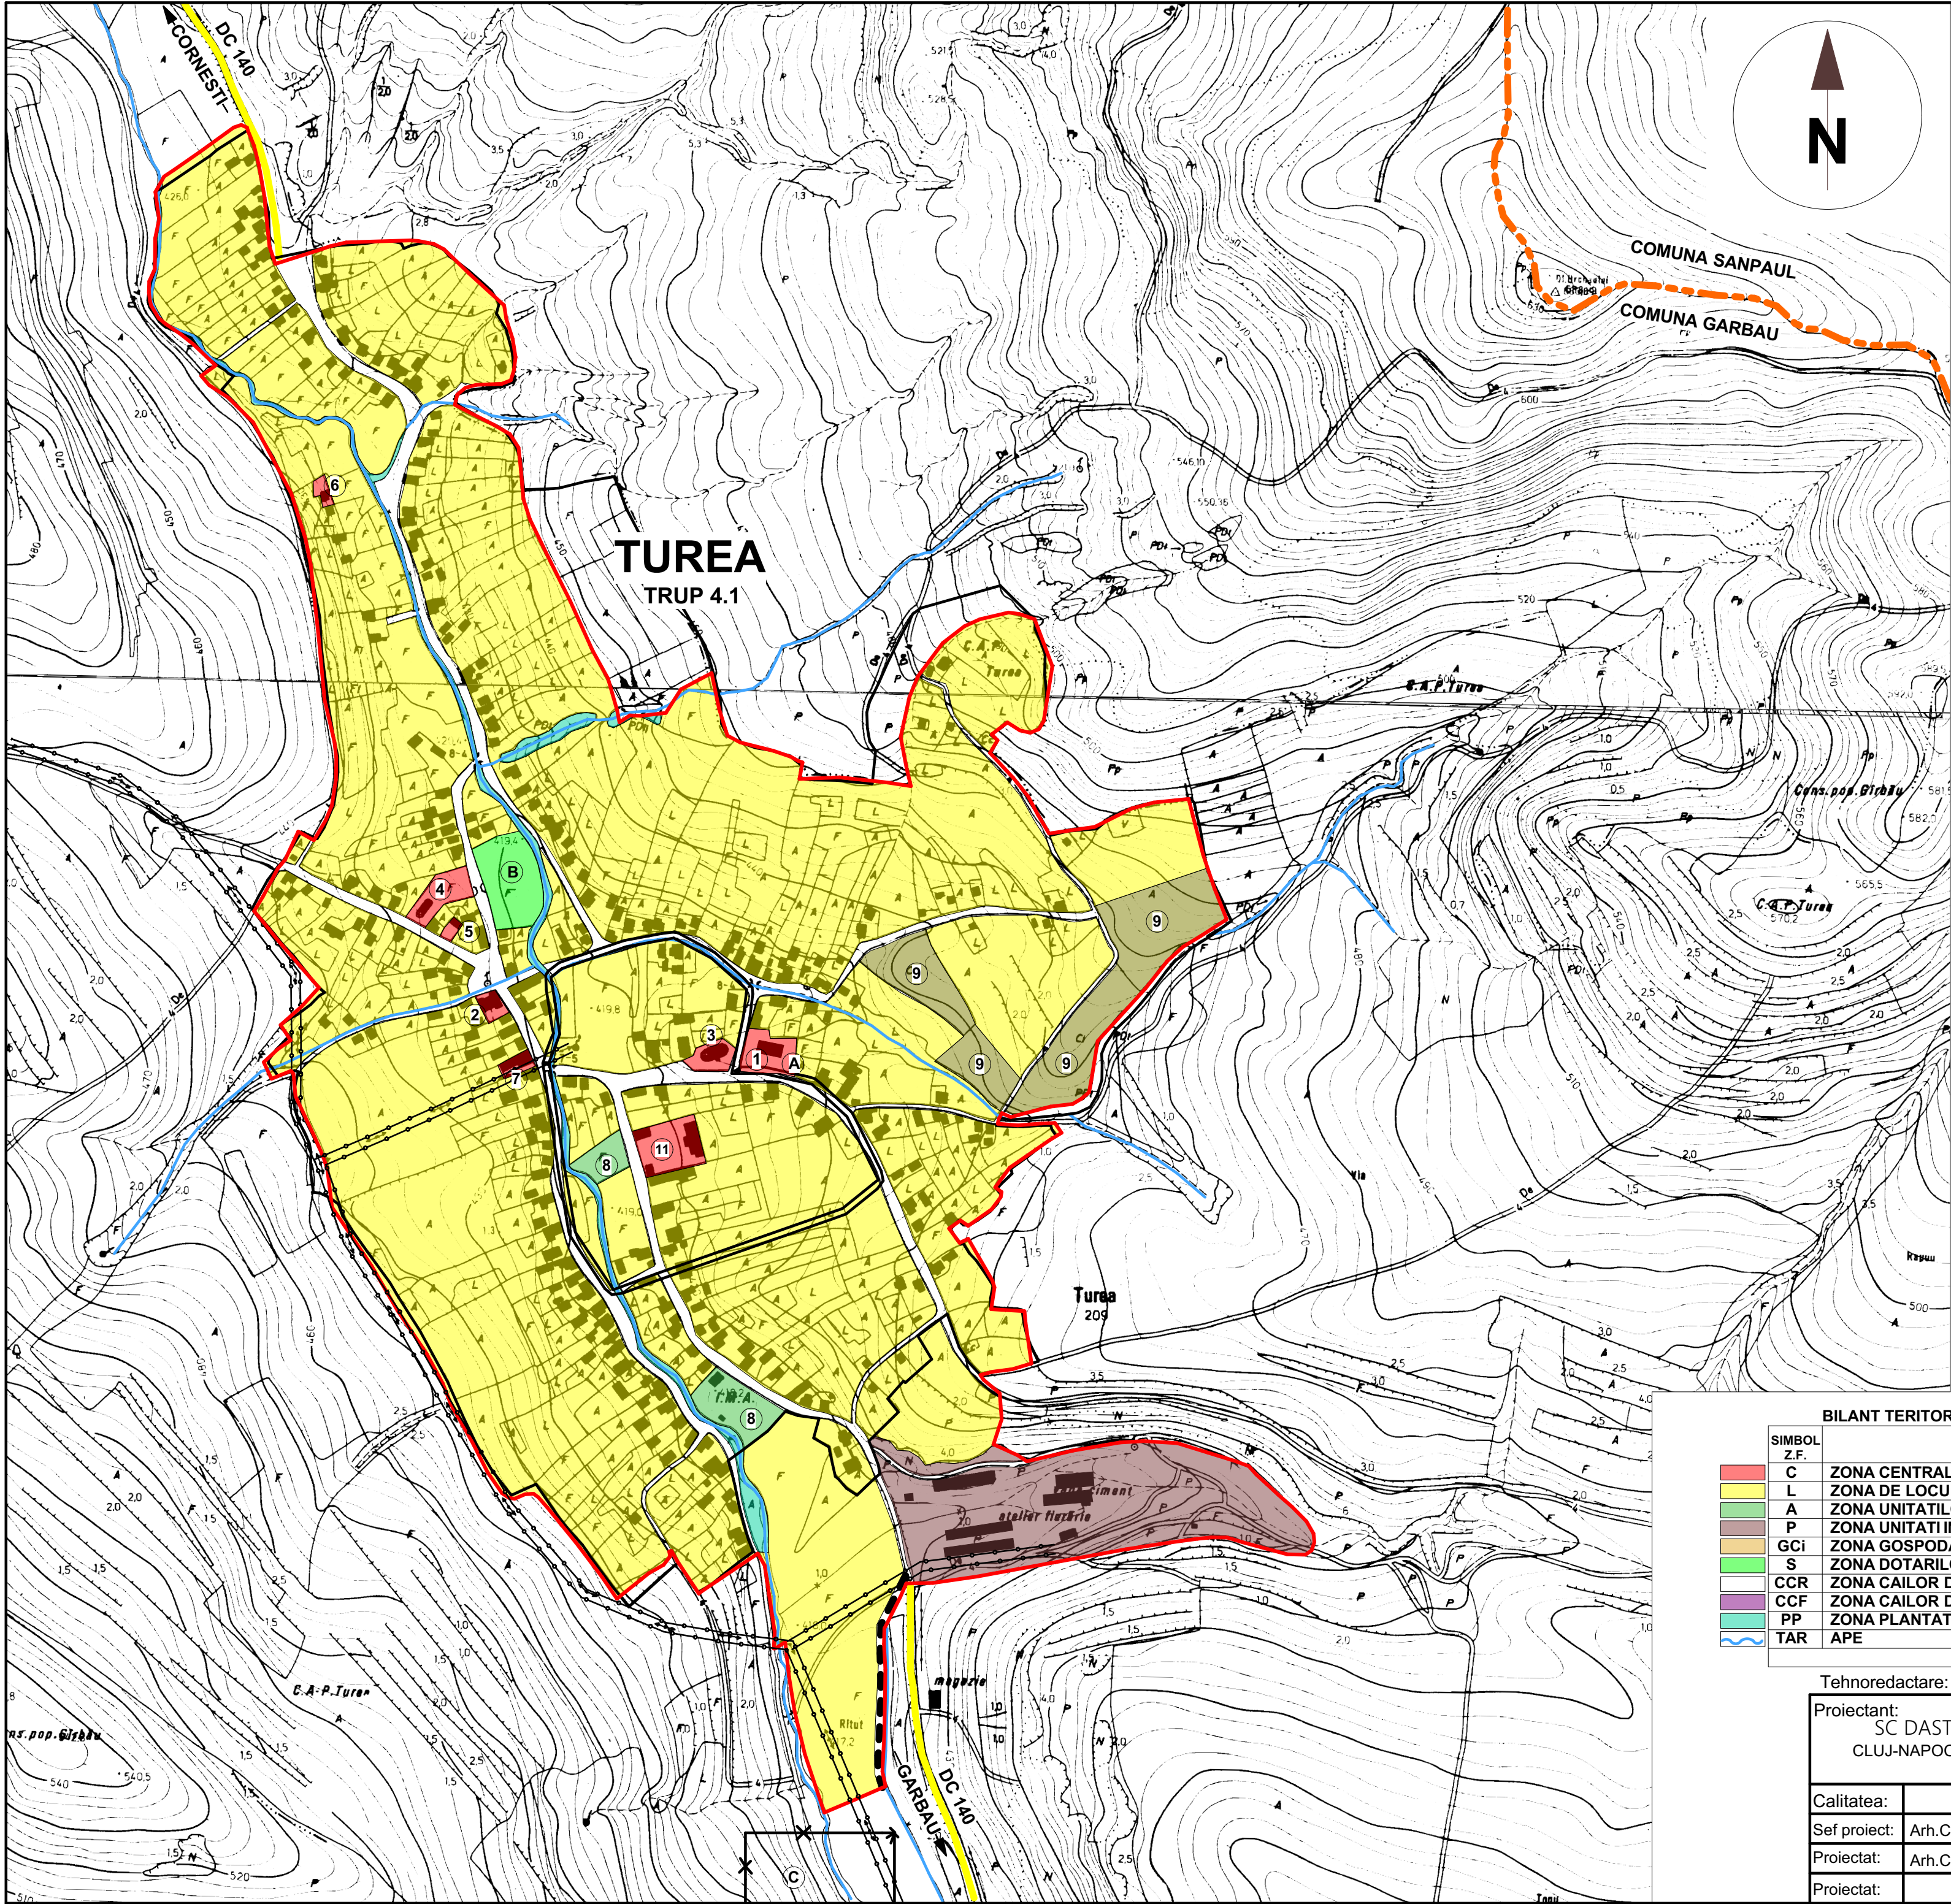

LEGENDA

LIMITE

- LIMITA INTRAVILANULUI 1990
- LIMITA INTRAVILANULUI 2010
- LIMITA TERITORIULUI ADMINISTRATIV AL COMUNEI
- LIMITA REZERVATIE NATURALA

ZONIFICARE FUNCTIONALA

- ZONA CENTRALA, FUNCTIUNI DE INTERES PUBLIC
- ZONA DE LOCUINTE SI FUNCTIUNI COMPLEMENTARE
- ZONA UNITATILOR AGRICOLE SI SILVICE
- ZONA UNITATI INDUSTRIALE, DEPOZITARE SI PRESTARI SERVICII
- ZONA GOSPODARIE COMUNALA, CIMITIRE
- ZONA DOTARILOR SPORTIVE SI DE AGREMENT
- ZONA CAILOR DE COMUNICATIE RUTIERA
- ZONA PLANTATIILOR DE PROTECTIE
- APE
- L 4.1 INDICATIV UTR

ZONE DE PROTECTIE / INTERDICTIE

- ZONA DE PROTECTIE FATADE OBIECTIVE CU VALOARE DE PATRIMONIU
- ZONA DE PROTECTIE PE BAZA NORMELOR SANITARE
- ZONA DE PROTECTIE FATADE CONSTRUCTII SI RELETE DE UTILITATI PUBLICE
- INTERDICTIE TEMPORARA DE CONSTRUIRE
- INTERDICTIE DEFINITIVA DE CONSTRUIRE

DRUMURI

- DRUMURI JUDETENE
- DRUMURI COMUNALE
- STRAZI PROPUSE PENTRU MODERNIZARE
- STRAZI PROPUSE PE TRASEE NOI

OBIECTIVE EXISTENTE

- 1 Scoala
- 2 Caminul cultural
- 3 Biserica Reformata
- 4 Biserica Ortodoxa
- 5 Biserica Adventista
- 6 Agentie Postala
- 7 Unitati comerciale
- 8 Unitati productie agroindustriala
- 9 Cimitir
- 10 Teren sport
- 11 Conacul Banffy - monument istoric

OBIECTIVE PROPUSE

- A Loc de joaca pentru copii
- B Teren de sport
- C Statie de epurare

BILANT TERITORIAL (ha)

SIMBOL Z.F.	ZONA FUNCTIONALA	EXISTENT		PROPOS	
		Supr.	%	Supr.	%
C	ZONA CENTRALA, FUNCTIUNI DE INTERES PUBLIC	1.20	1.43	1.20	1.31
L	ZONA DE LOCUINTE SI FUNCTIUNI COMPLEMENTARE	74.06	88.08	76.30	83.52
A	ZONA UNITATILOR AGRICOLE SI SILVICE	0.63	0.75	0.63	0.69
P	ZONA UNITATI INDUSTRIALE, DEPOZITARE SI PRESTARI SERVICII	-	-	4.81	5.27
GCI	ZONA GOSPODARIE COMUNALA, CIMITIRE	2.83	3.37	2.83	3.10
S	ZONA DOTARILOR SPORTIVE SI DE AGREMENT	-	-	0.58	0.63
CCR	ZONA CAILOR DE COMUNICATIE RUTIERA	3.16	3.76	4.00	4.38
CCF	ZONA CAILOR DE COMUNICATIE FERVIARA	-	-	-	-
PP	ZONA PLANTATIILOR DE PROTECTIE	1.24	1.47	1.24	1.36
TAR	APE	0.96	1.14	0.96	1.05
TOTAL		84.08	100	91.35	100

Tehnoredactare: S.C. CIULEI PROIECT S.R.L.

Proiectant: SC DAST COMSERV SRL CLUJ-NAPOCA, STR. MARINESCU, NR.7 J12/2020/1994			Beneficiar: COMUNA GARBAU JUDETUL CLUJ		Pr. Nr.: 61 2010
Calitatea:	Numele:	Semnatura:	Data: Sept 2010	Obiect: PLAN URBANISTIC GENERAL AL COMUNEI GARBAU, JUD. CLUJ - ACTUALIZARE 2010	PUG
Sef proiect:	Arh.Cosoveanu Sorin				
Proiectat:	Arh.Cosoveanu Sorin		Scara: 1:5 000	Denumire Planşa: Sat TUREA REGLEMENTARI	Plansa: 3.4
Proiectat:					